


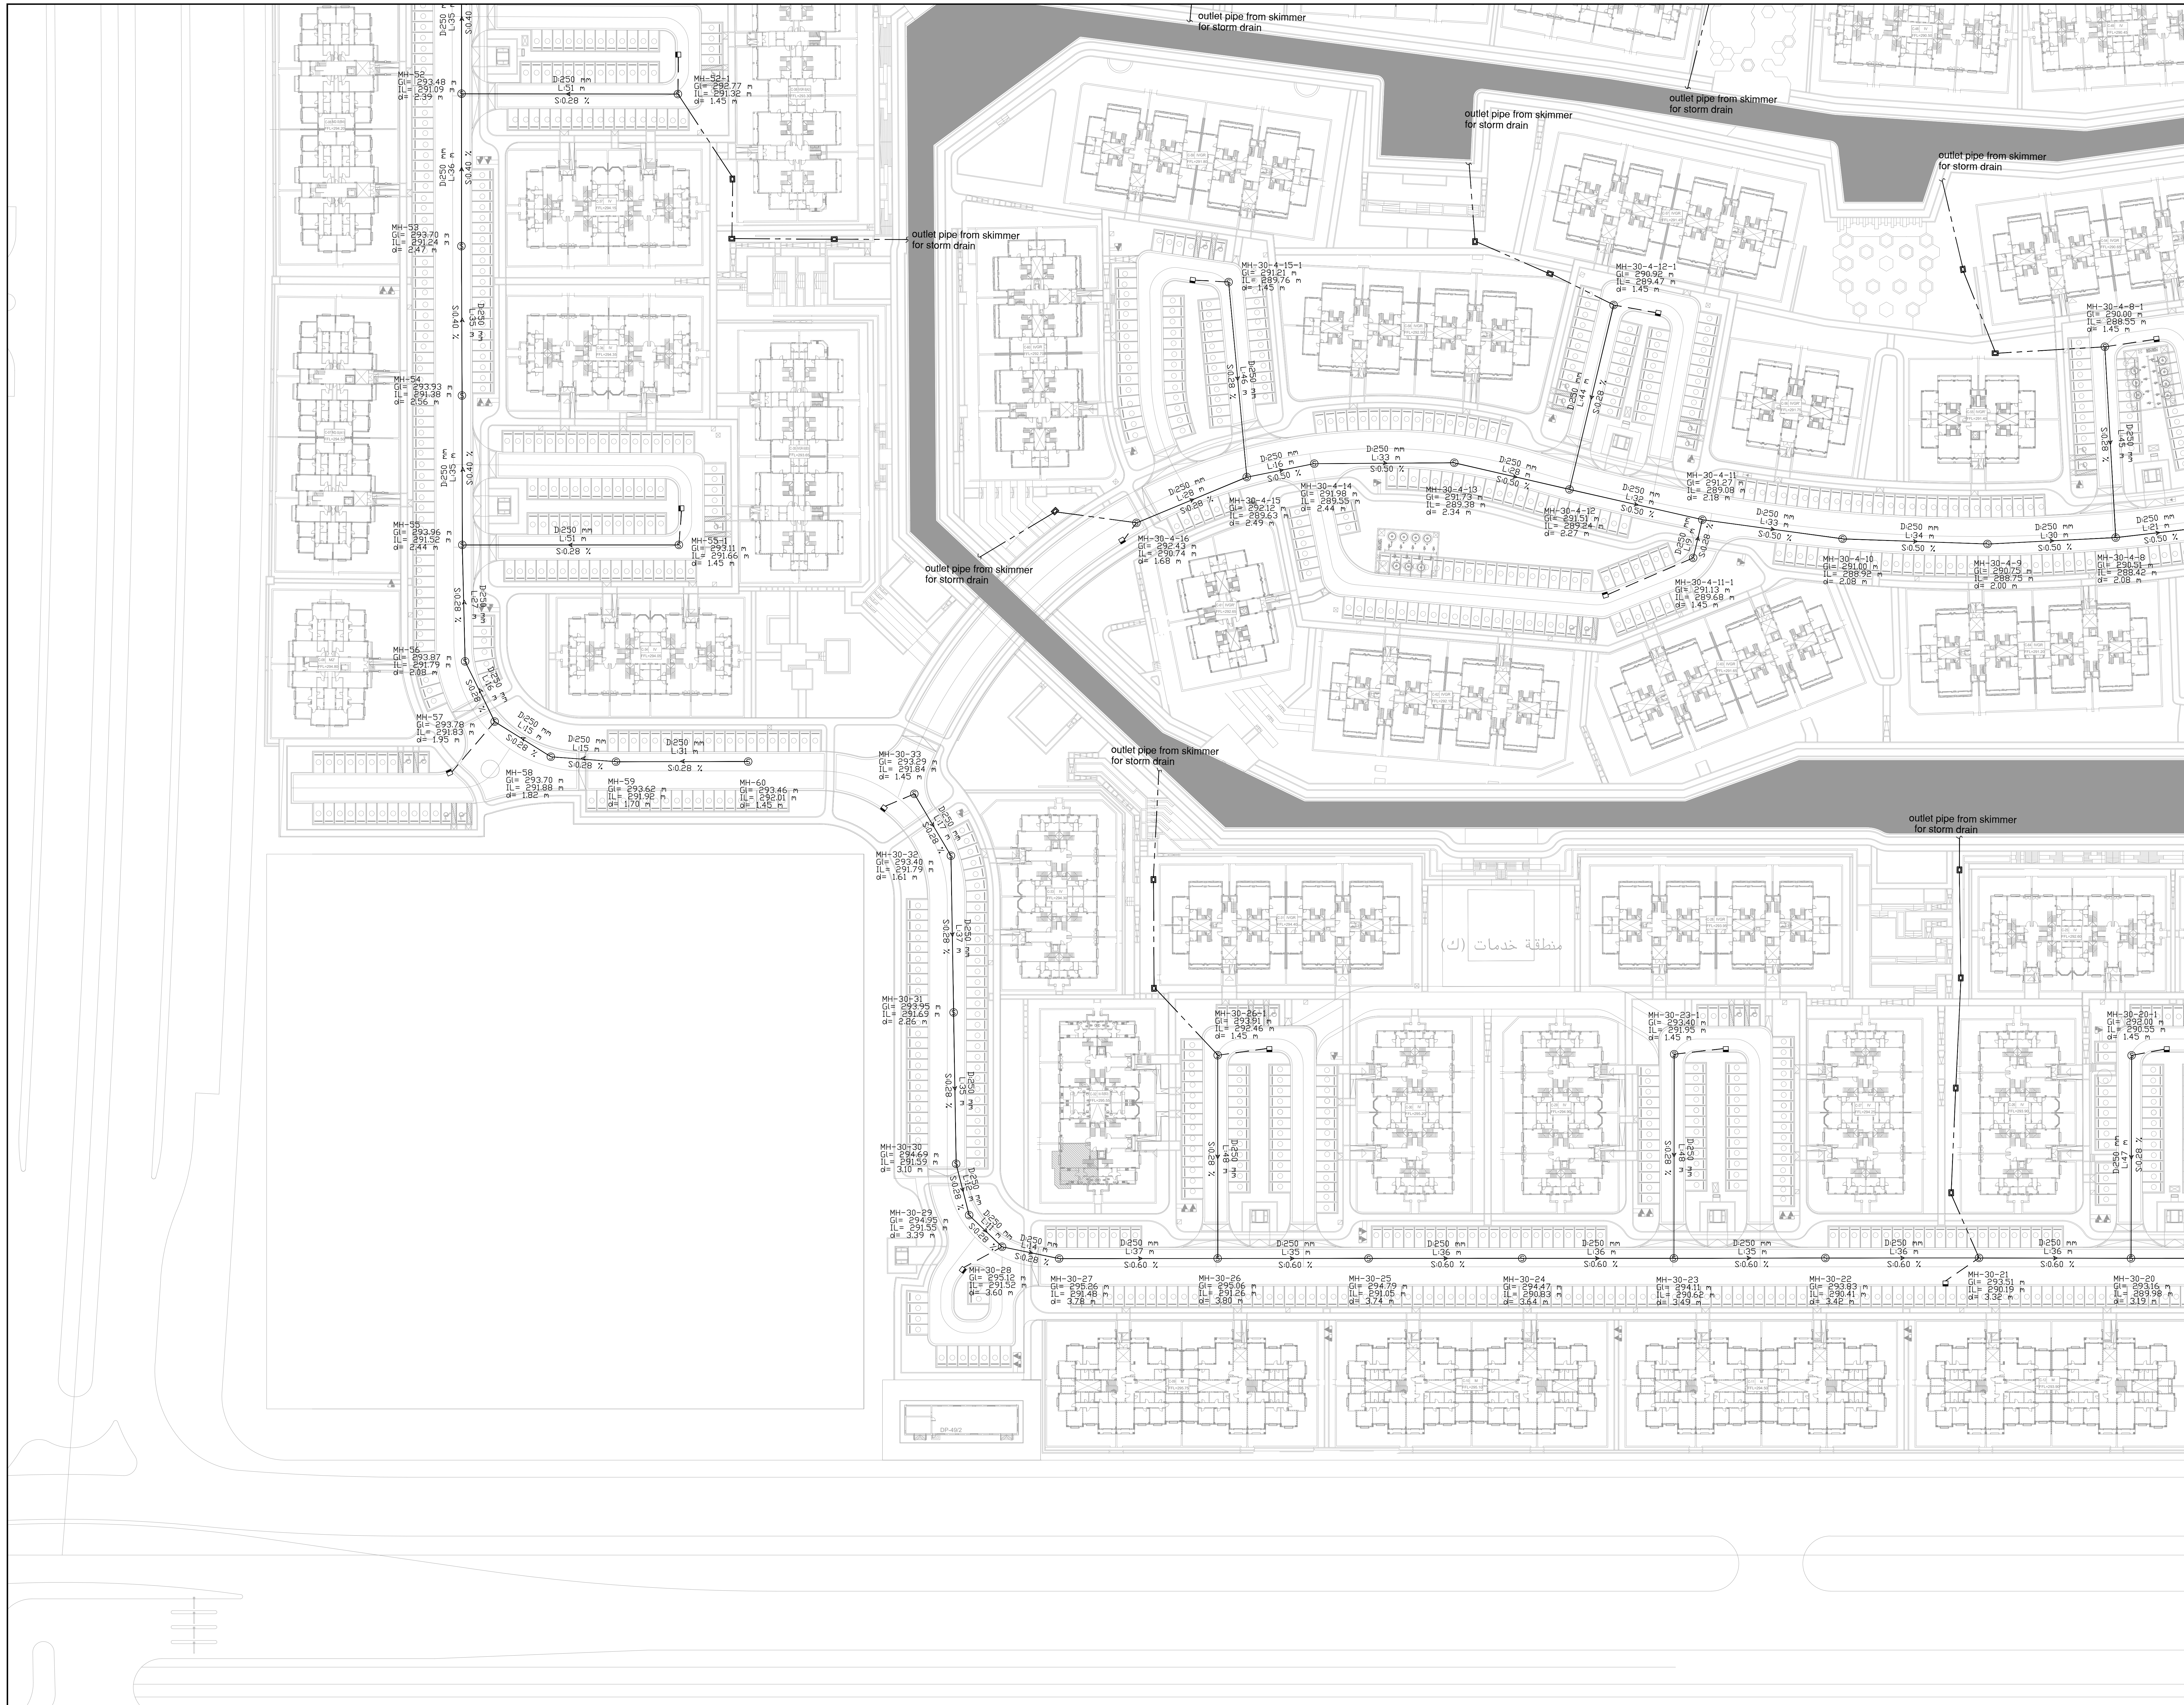

NOTES

- PIPE DIAMETERS ARE SHOWN IN MILLIMETERS FOR NOMINAL DIAMETERS UNLESS OTHERWISE INDICATED.
- ALL PIPES ARE HOPE WITH STANDING PRESSURE 6 BARS.
- PIPES SHALL BE LAID SUCH THAT THE MINIMUM SOIL COVER OVER PIPE NOT LESS THAN 1.20 m.
- THE CONTRACTOR SHOULD COORDINATE WITH OTHER UTILITIES DURING SITE CONSTRUCTION.
- THE CONTRACTOR SHOULD COORDINATE FINAL LOCATION OF MANHOLES WITH STRUCTURE FOUNDATION.
- ALL MANHOLES IN HARDSCAPE SHOULD BE WITH DECORATION COVER MATCH WITH THE SURROUNDING LOCATION.
- PIPES BEHIND PLANTS SHOULD BE PLACED INSIDE A CONCRETE ENCASUREMENT TO PROTECT PIPES FROM PLANT ROOTS.
- EXACT LOCATION OF CATCH BASIN SHOULD BE JUSTIFIED BY CONTRACTOR ON SHOP DRAWINGS.
- COVERS FOR MANHOLES, INSPECTION CHAMBERS, SLOW DOWN CHAMBERS & CATCH BASINS TO BE RATED FOR (40 TON LOAD) IF INSTALLED IN ROWWAYS OR PARKING AREAS, AND TO BE RATED FOR (25 TON LOAD) IF INSTALLED IN LANDSCAPE AREAS OR SIDE WALKS.
- FOR THE FINAL LOCATIONS OF INSPECTION CHAMBERS, FIRE HYDRANTS, WATER TANKS, PUMP ROOMS AND LIFT STATIONS REFER TO MASTER PLAN AND LANDSCAPE DRAWINGS.

LEGEND

- PROPOSED STORM PIPE
- PROPOSED FORCE MAIN
- CATCH BASIN PIPE - 160 mm
- SKIMMER DRAIN PIPE - 160 mm
- STORM MANHOLE
- CATCH BASIN
- INSPECTION CHAMBER 60"x90" Cm

KEY PLAN:

REV	DESCRIPTION	DATE
00	ISSUED FOR TENDER	JAN 2026

CLIENT: MOUNTAIN VIEW
CITY STAGE, DEVELOPMENTAL STAGE BY STAGE CAPITAL SA
THE DEVELOPMENT OF LANDSCAPE, CIVIL, MECHANICAL, ELECTRICAL, AND SANITARY
TEL: 002 482 1111 E-MAIL: PAK@02 482 1111 F-MAIL: 002 482 1111

PROJECT NAME: **ALIVA**
PHASE 01

CONSULTANTS: DMA
DESIGN | ENGINEERING
87 El Mostahar Almadani Street, Shoubra El-Kheayma, El-Nouba, Cairo, Egypt
Tel: +902 2269 7960 / +902 2269 8305 Web: www.dma.com.eg

SHEET TITLE: **STORM NETWORK PART (2/6)**

SHEET REFERENCE NO.	DRW	RSS	DSN	ZME
AL-C-SR-122	CHK	RSS	APRV	HMS
PROJECT NO	DMA-14-040-000			
SHEET SERIAL NO.	03 OF 07	REVISION NO	00	