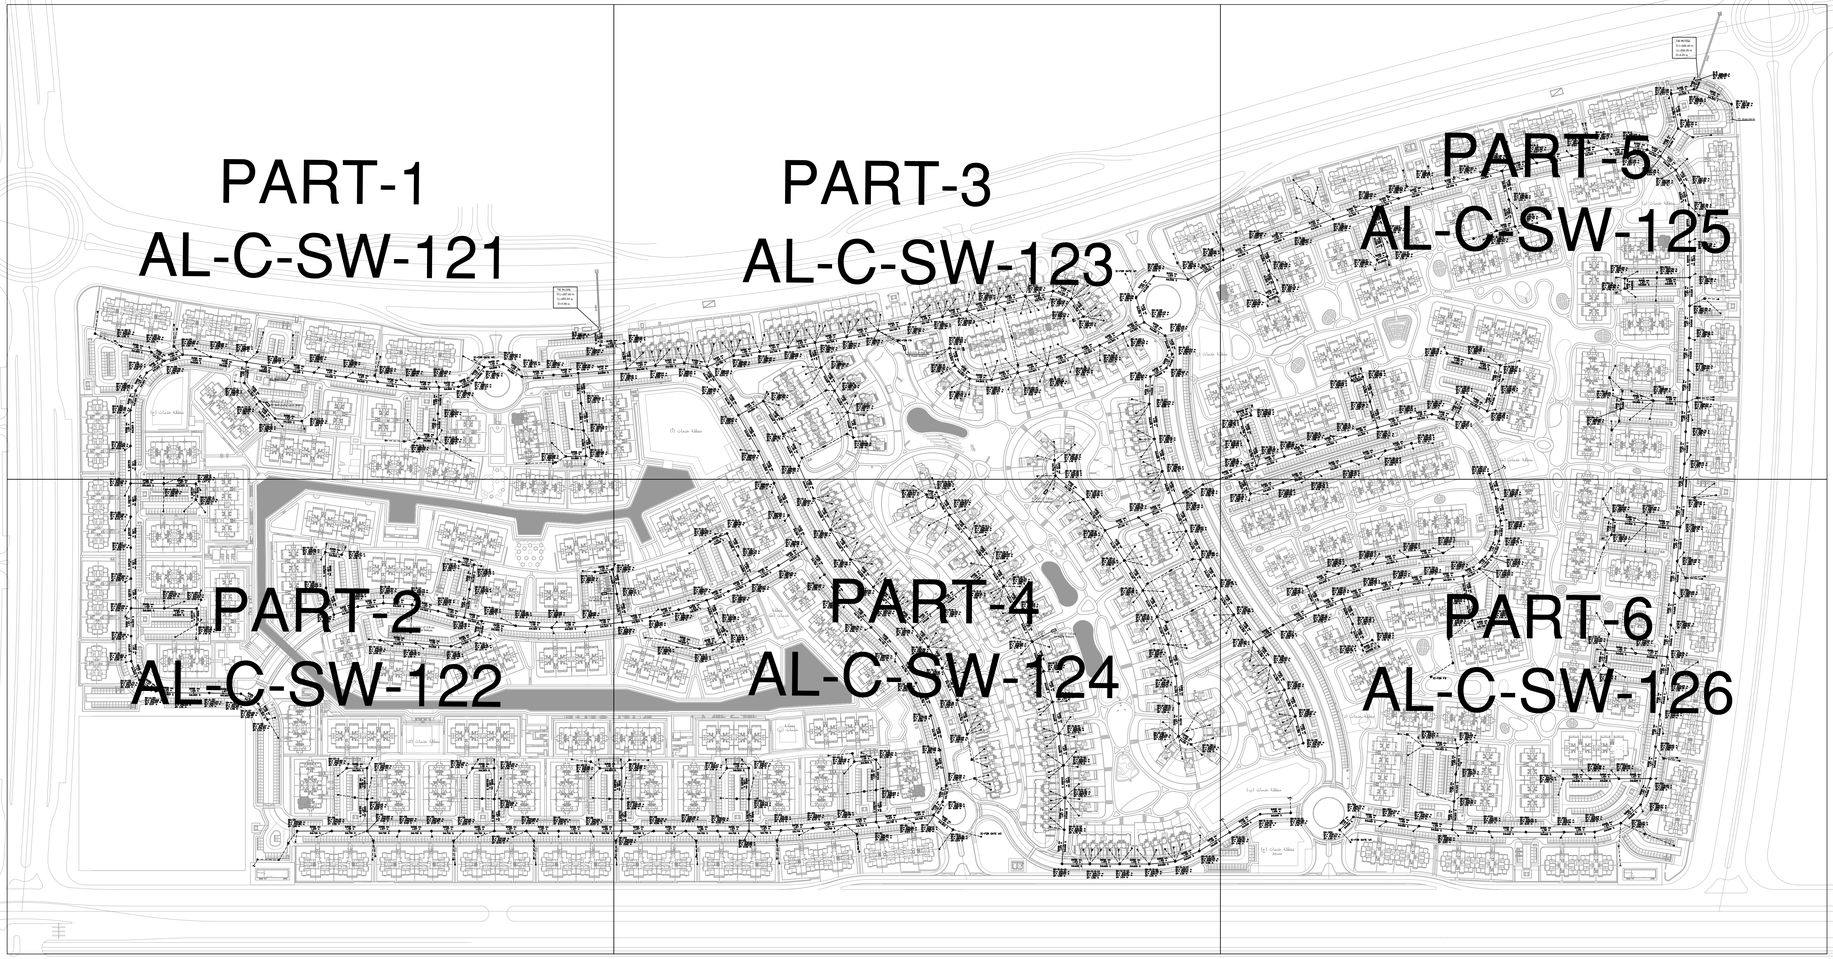



NOTES

1. PIPE DIAMETERS ARE SHOWN IN MILLIMETERS FOR NOMINAL DIAMETERS UNLESS OTHERWISE INDICATED.
2. ALL PIPES ARE HDPE WITH STANDING PRESSURE 6 BARS.
3. PIPES SHALL BE LAID SUCH THAT THE MINIMUM SOIL COVER OVER PIPE NOT LESS THAN 1.20 m.
4. THE CONTRACTOR SHOULD COORDINATE WITH OTHER UTILITIES DURING SITE CONSTRUCTION
5. THE CONTRACTOR SHOULD COORDINATE FINAL LOCATION OF MANHOLES WITH STRUCTURE FOUNDATION
6. THE CONTRACTOR SHOULD COORDINATE THE FINAL LOCATION OF THE SEWER TIE INS ACCORDING TO SITE CONDITION.
7. All MANHOLES IN HARDSCAPE SHOULD BE WITH DECORATION COVER MATCH WITH THE SURROUNDING LOCATION.
8. PIPES BESIDE PLANTS SHOULD BE PLACED INSIDE A CONCRETE ENCASEMENT TO PROTECT PIPES FROM PLANT ROOTS.
9. ALL BUILDINGS TIE-IN DIAMETER SHALL BE ACCORDING TO PLUMING DESIGN.
10. EXACT LOCATION OF CATCH BASIN SHOULD BE JUSTIFIED BY CONTRACTOR ON SHOP DRAWINGS.
11. COVERS FOR MANHOLES ,INSPECTION CHAMBERS, SLOW DOWN CHAMBERS & CATCH BASINS TO BE RATED FOR (40 TON LOAD) IF INSTALLED IN ROADWAYS OR PARKING AREAS , AND TO BE RATED FOR (25 TON LOAD) IF INSTALLED IN LANDSCAPE AREAS OR SIDE WALKS.
12. FOR THE FINAL LOCATIONS OF INSPECTION CHAMBERS ,FIRE HYDRANTS, WATER TANKS, PUMP ROOMS AND LIFT STATIONS REFER TO MASTER PLAN AND LANDSCAPE DRAWINGS.

LEGEND

- PROPOSED SEWAGE PIPE
- PROPOSED FORCE MAIN
- SEWAGE PIPE - 160 mm
- SEWAGE MANHOLE
- SLOW DOWN CHAMBER
- INSPECTION CHAMBER FROM PLUMING WORK
- INSPECTION CHAMBER 60 *60 Cm
- INSPECTION CHAMBER 60 *90 Cm

KEY PLAN:

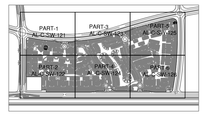

REV	DESCRIPTION	DATE
00	ISSUED FOR TENDER	JAN.2026

CLIENT:

MOUNTAIN VIEW
a place to look up to

CITY STARS , OMAR BN EL KATAB ST. STAR CAPITAL AL
2ND FLOOR,NAT NO. 24 HELIOPOLIS , CAIRO, EGYPT
TEL:+202 480 1111 E- FAX:+202 480 1113 - MOB: +2 0170 17 41

PROJECT NAME:

ALIVA
PHASE 01

CONSULTANTS:

DMA
DESIGN | ENGINEERING
87 El Mosheer Ahmed Ismail St, Sheraton District, El Nozha, Cairo, Egypt
Tel: +202 2269 7586 / +202 2269 6308 Web: www.dma.com.eg

SHEET TITLE:

SEWAGE NETWORK
KEY PLAN

SHEET REFERENCE NO:					
AL-C-SW-120	DRW	ZME	DSN	ZME	
	CHK	RSS	APRV	HMS	
	SCALE	1:2000			
	PROJECT NO	DMA-I-M-040-000			
SHEET SERIAL NO. ## OF 07	REVISION NO	00			

COPYRIGHT NOTICE: THIS DRAWING AND ALL INFORMATION WITHIN ARE THE SOLE PROPERTY OF DMA CONSULTANTS. UNAUTHORIZED COPYING, REPRODUCTION, REDISTRIBUTION, OR USE OF THIS INFORMATION, IN WHOLE OR IN PART, WITHOUT WRITTEN CONSENT OF THE DMA CONSULTANTS, IS STRICTLY PROHIBITED. VIOLATIONS ARE LABEL FOR PROSECUTION UNDER THE EGYPTIAN AND INTERNATIONAL LAWS OF COPYRIGHT. © 2011 DMA CONSULTANTS ALL RIGHTS RESERVED

A0