

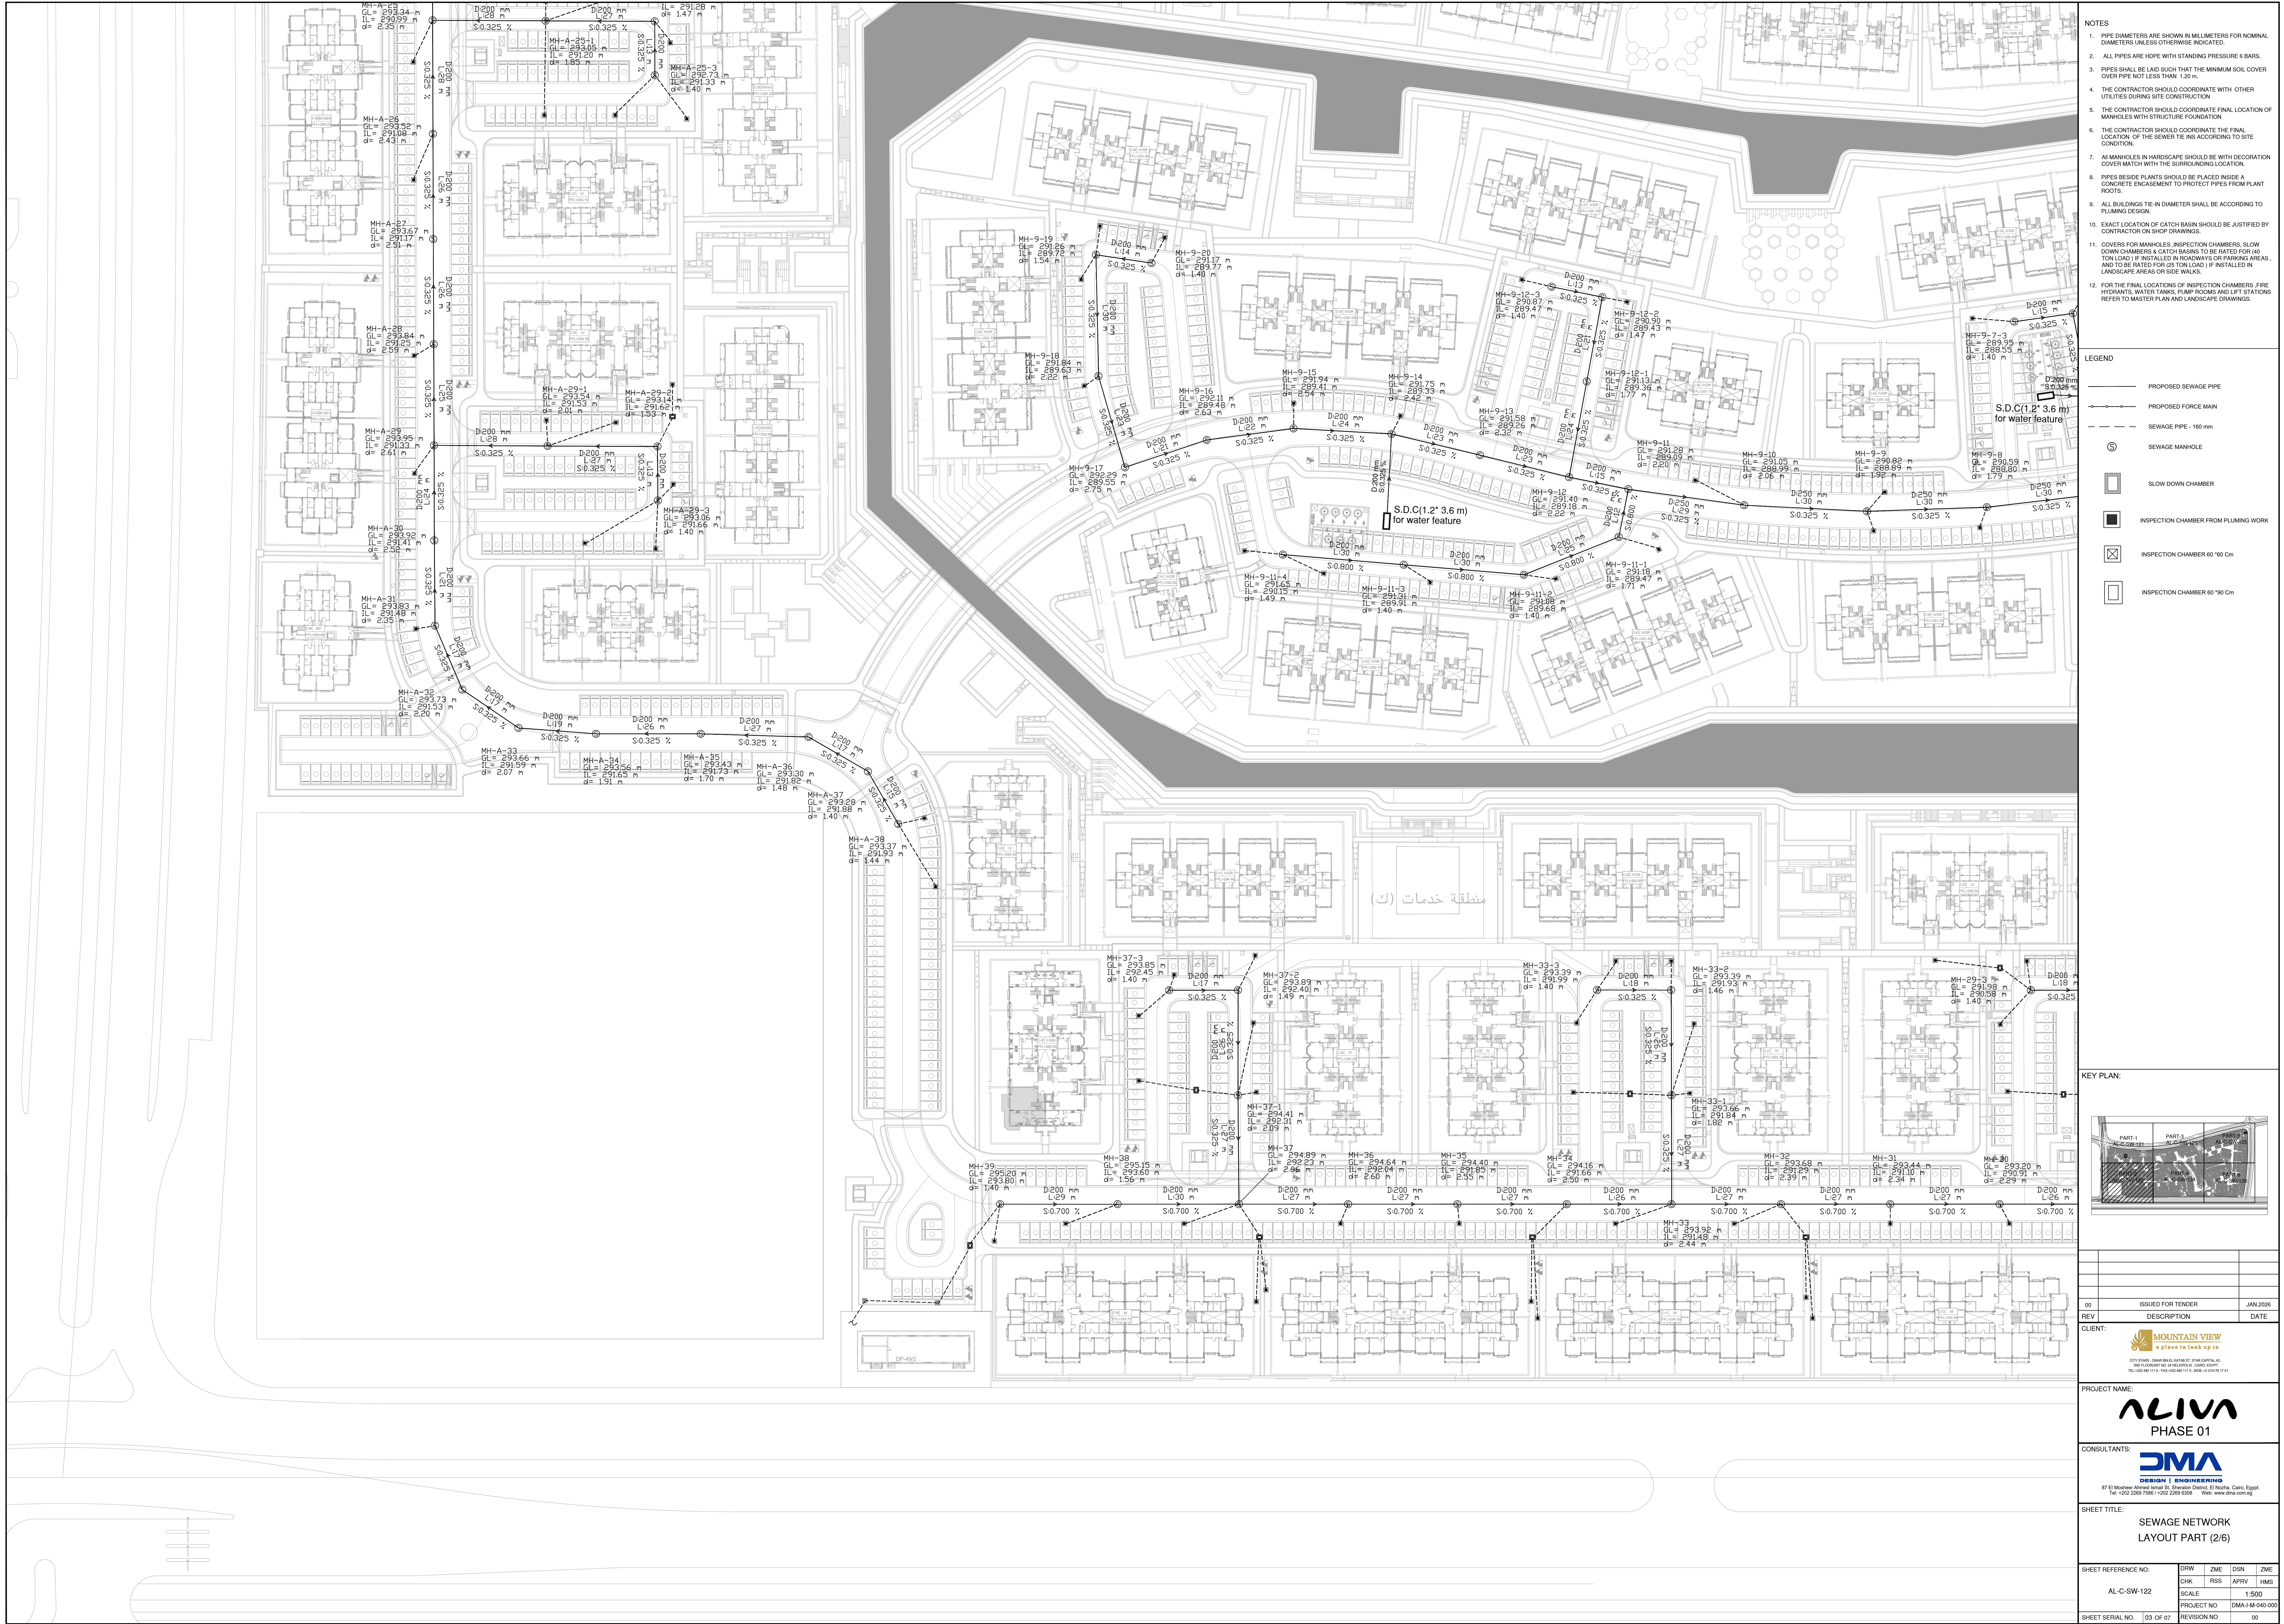


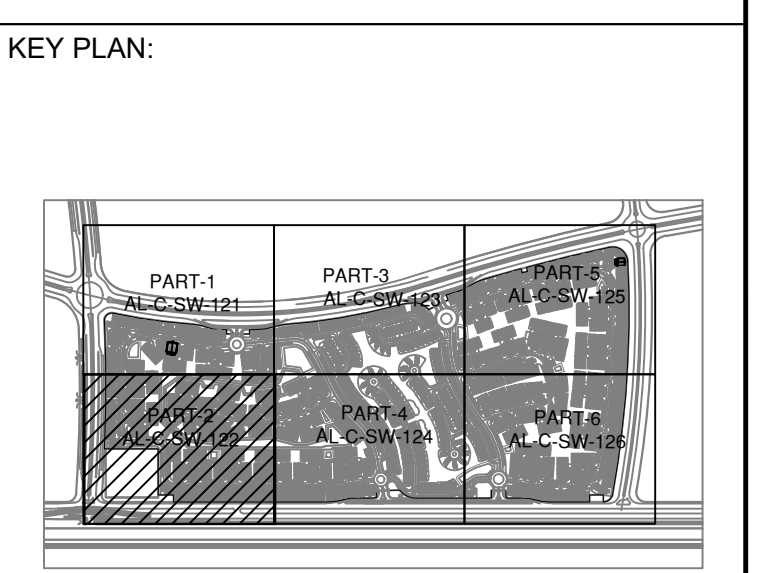

- NOTES
1. PIPE DIAMETERS ARE SHOWN IN MILLIMETERS FOR NOMINAL DIAMETERS UNLESS OTHERWISE INDICATED.
 2. ALL PIPES ARE HOPE WITH STANDING PRESSURE 6 BARS.
 3. PIPES SHALL BE LAID SUCH THAT THE MINIMUM SOIL COVER OVER PIPE NOT LESS THAN 1.20 m.
 4. THE CONTRACTOR SHOULD COORDINATE WITH OTHER UTILITIES DURING SITE CONSTRUCTION.
 5. THE CONTRACTOR SHOULD COORDINATE FINAL LOCATION OF MANHOLES WITH STRUCTURE FOUNDATION.
 6. THE CONTRACTOR SHOULD COORDINATE THE FINAL LOCATION OF THE SEWER TIE INS ACCORDING TO SITE CONDITION.
 7. ALL MANHOLES IN HARDSCAPE SHOULD BE WITH DECORATION COVER MATCH WITH THE SURROUNDING LOCATION.
 8. PIPES BESIDE PLANTS SHOULD BE PLACED INSIDE A CONCRETE ENCASMENT TO PROTECT PIPES FROM PLANT ROOTS.
 9. ALL BUILDINGS TIE-IN DIAMETER SHALL BE ACCORDING TO PLUMBING DESIGN.
 10. EXACT LOCATION OF CATCH BASIN SHOULD BE JUSTIFIED BY CONTRACTOR ON SHOP DRAWINGS.
 11. COVERS FOR MANHOLES, INSPECTION CHAMBERS, SLOW DOWN CHAMBERS & CATCH BASINS TO BE RATED FOR 40 TON LOAD IF INSTALLED IN ROADWAYS OR PARKING AREAS, AND TO BE RATED FOR (25 TON LOAD) IF INSTALLED IN LANDSCAPE AREAS OR SIDE WALKS.
 12. FOR THE FINAL LOCATIONS OF INSPECTION CHAMBERS, FIRE HYDRANTS, WATER TANKS, PUMP ROOMS AND LIFT STATIONS REFER TO MASTER PLAN AND LANDSCAPE DRAWINGS.

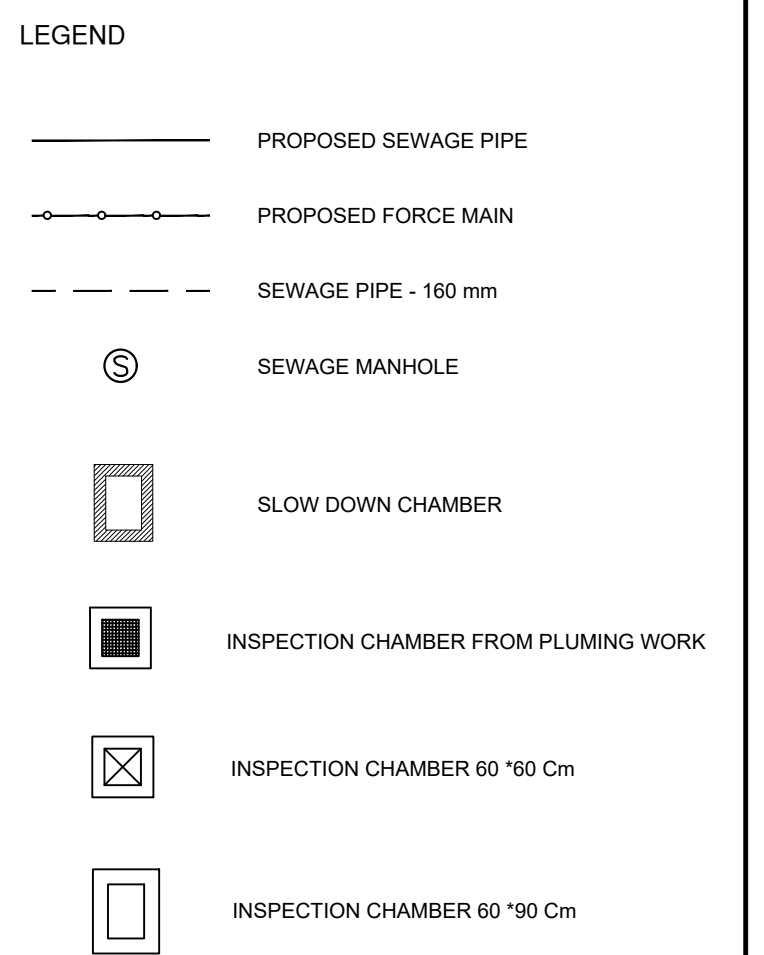

00	ISSUED FOR TENDER		JAN.2020
REV	DESCRIPTION		DATE
CLIENT:			
 MOUNTAIN VIEW a place to look up to CITY OFFICE, DAMEN MANSION BY STADIUM CAPITAL, EL DOKKI, EL DOKKI DISTRICT, EL HELWAN GOV, EGYPT TEL: 002 2258 7585 / 002 2258 8335 / Web: www.dma.com.eg			
PROJECT NAME:			
 PHASE 01			
CONSULTANTS:			
 DESIGN ENGINEERING 87 El Mostakim Street, El Shorouk District, El Helwan, Cairo, Egypt Tel: 002 2258 7585 / 002 2258 8335 / Web: www.dma.com.eg			
SHEET TITLE:			
SEWAGE NETWORK LAYOUT PART (2/6)			
SHEET REFERENCE NO:			
AL-C-SW-122			
DRW			
ZME			
DSN			
ZME			
CHK			
RSS			
APPR			
HMS			
SCALE			
1:500			
PROJECT NO			
DMA-J-M-040-000			
SHEET SERIAL NO:			
03 OF 07			
REVISION NO			
00			

COPYRIGHT NOTICE: THIS DRAWING AND ALL INFORMATION WITHIN ARE THE SOLE PROPERTY OF DMA CONSULTANTS. UNAUTHORIZED COPYING, REPRODUCTION, REDISTRIBUTION, OR USE OF THIS INFORMATION, IN WHOLE OR IN PART, WITHOUT WRITTEN CONSENT OF THE DMA CONSULTANTS, IS STRICTLY PROHIBITED. VIOLATIONS ARE LABEL FOR PROSECUTION UNDER THE EGYPTIAN AND INTERNATIONAL LAWS OF COPYRIGHT. © 2011 DMA CONSULTANTS ALL RIGHTS RESERVED