

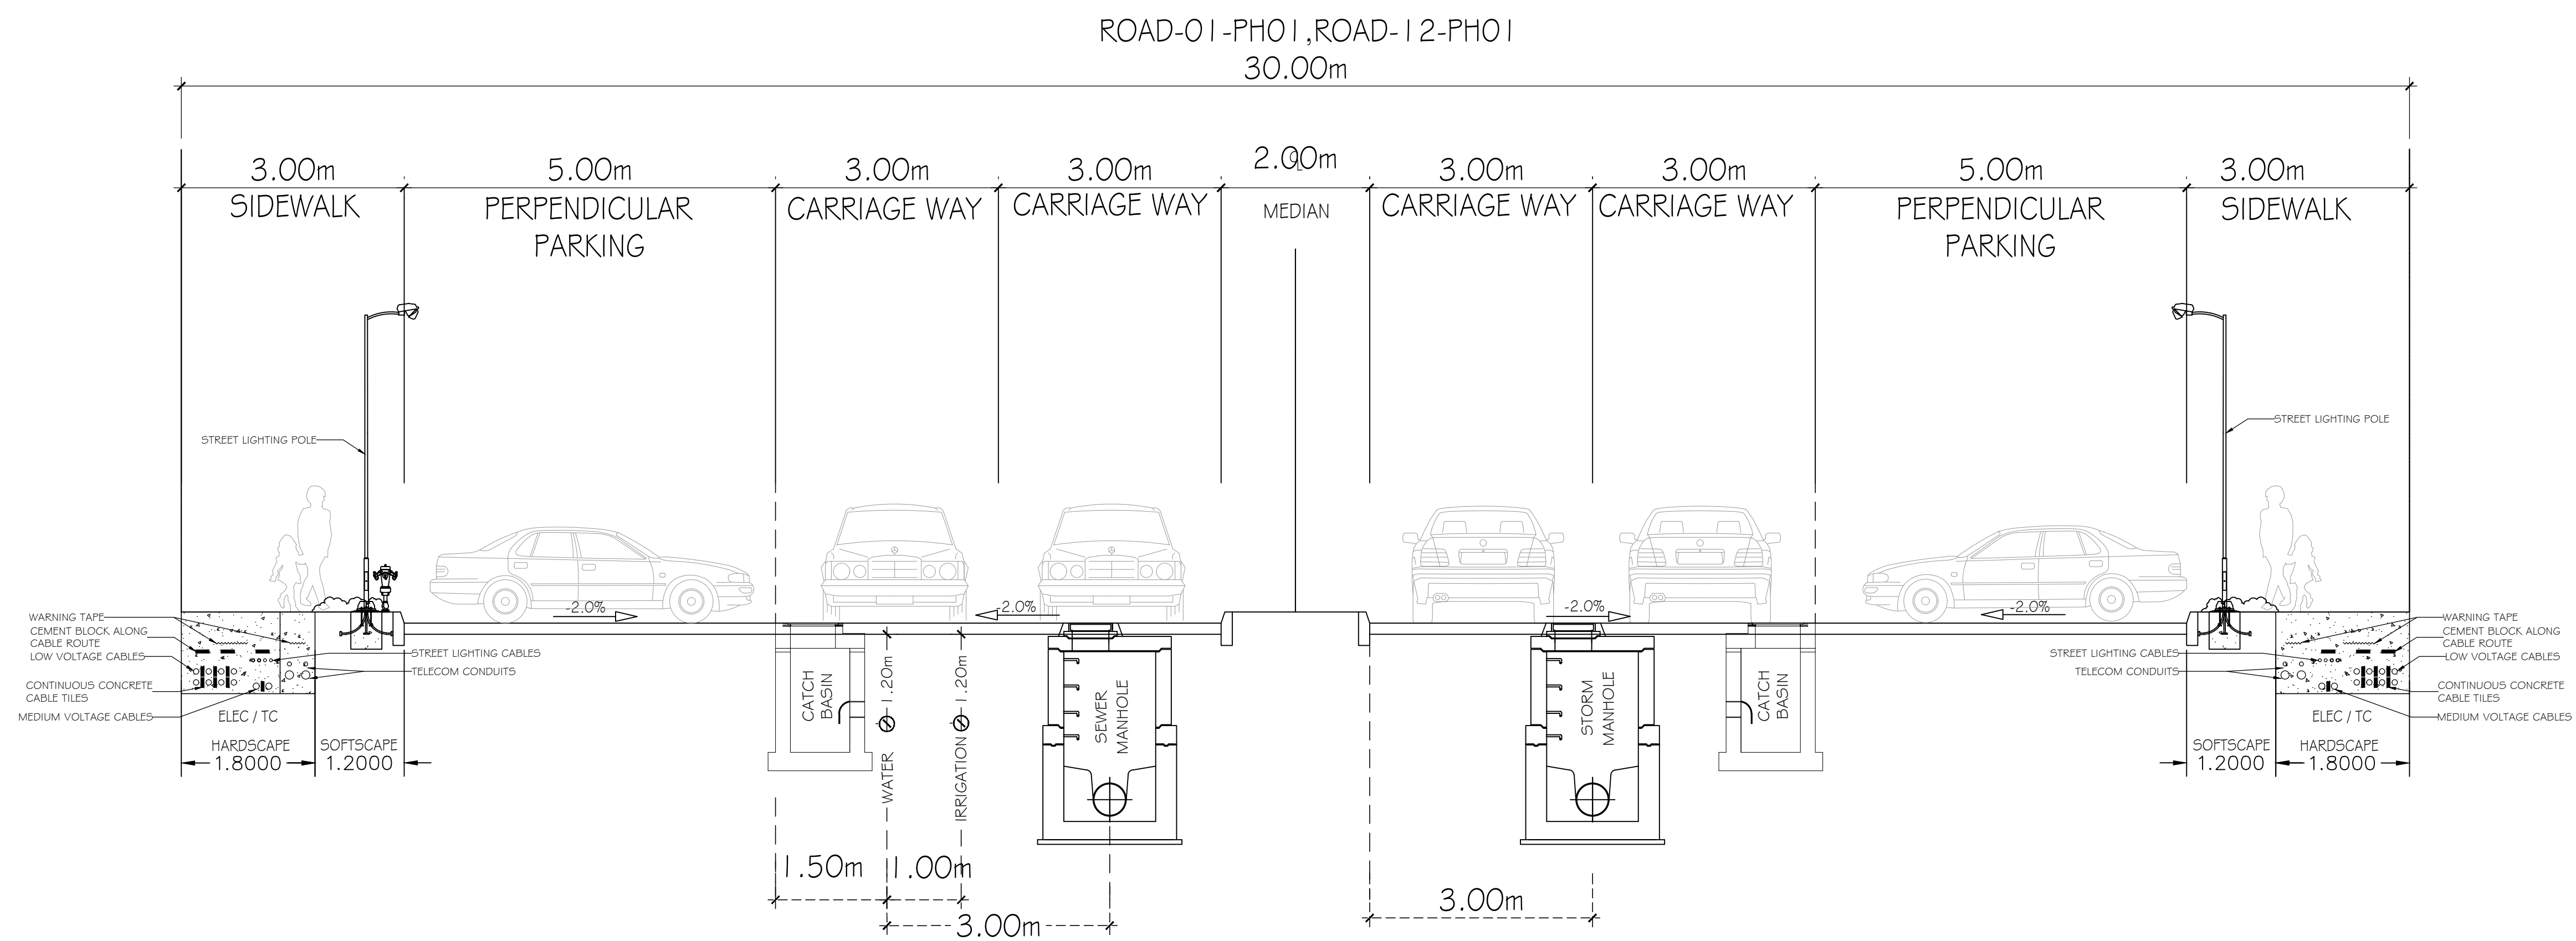


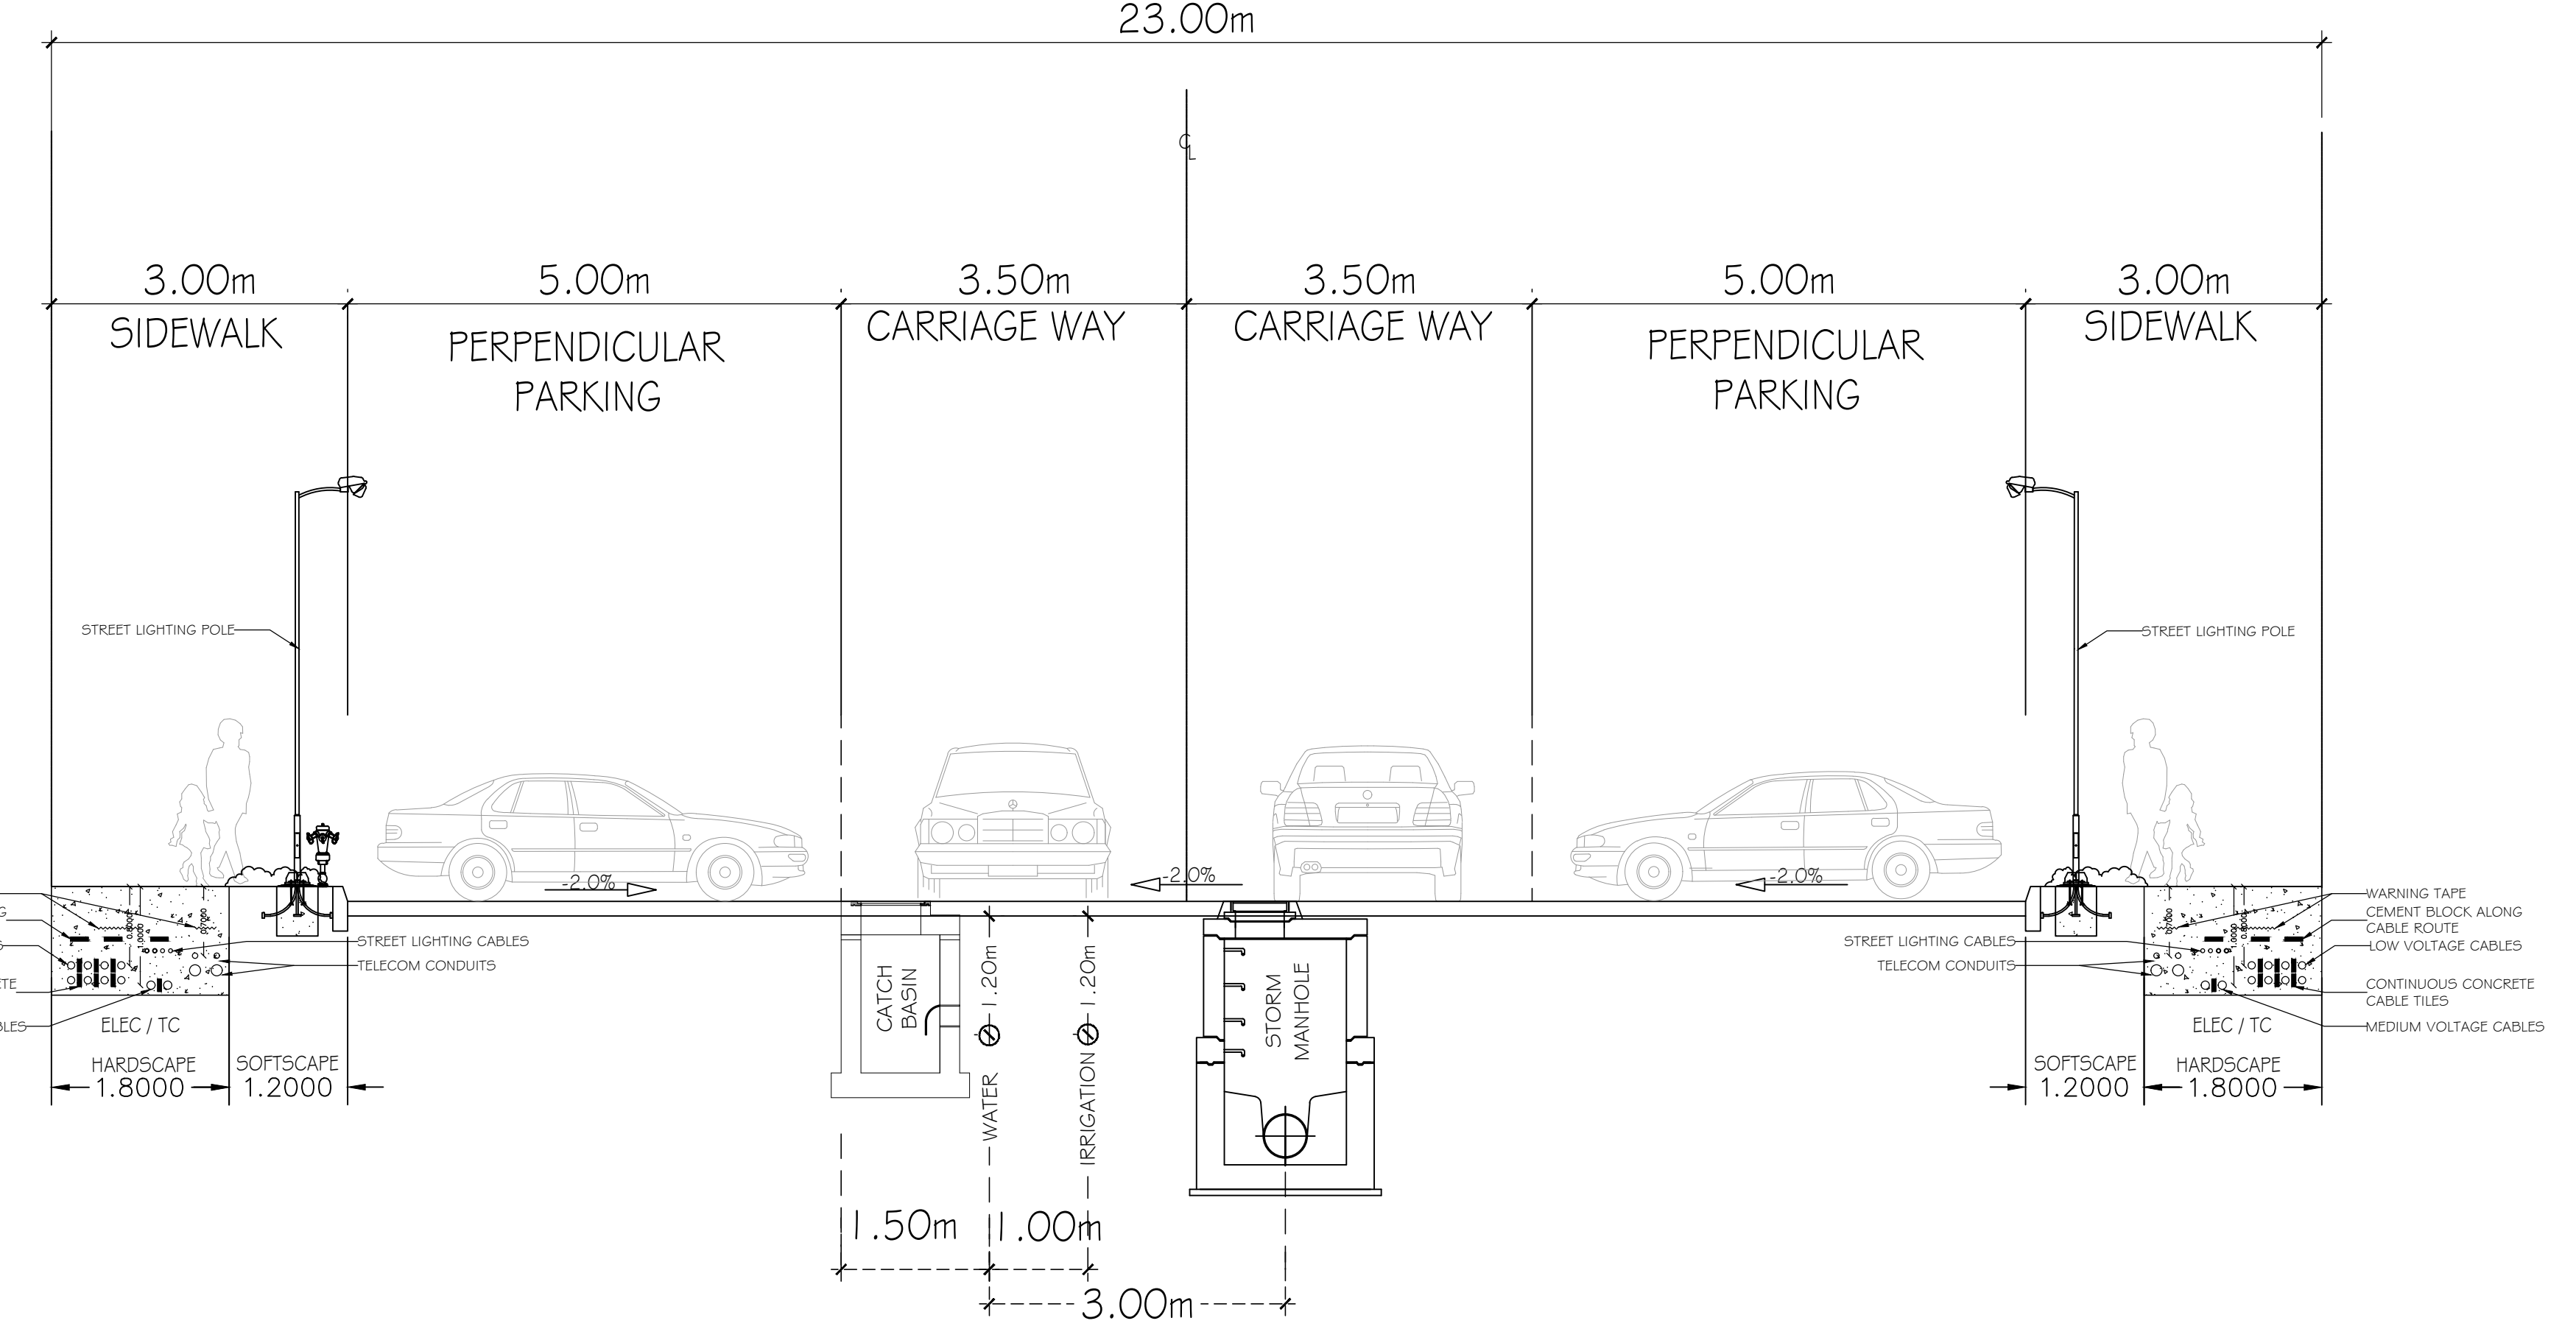

PARKING-04-PHO1, PARKING-08-PHO1, PARKING-10-PHO1, PARKING-25-PHO1, PARKING-27-PHO1, PARKING-37-PHO1

ROAD-02-PHO1, ROAD-03-PHO1, ROAD-18-PHO1, ROAD-19-PHO1

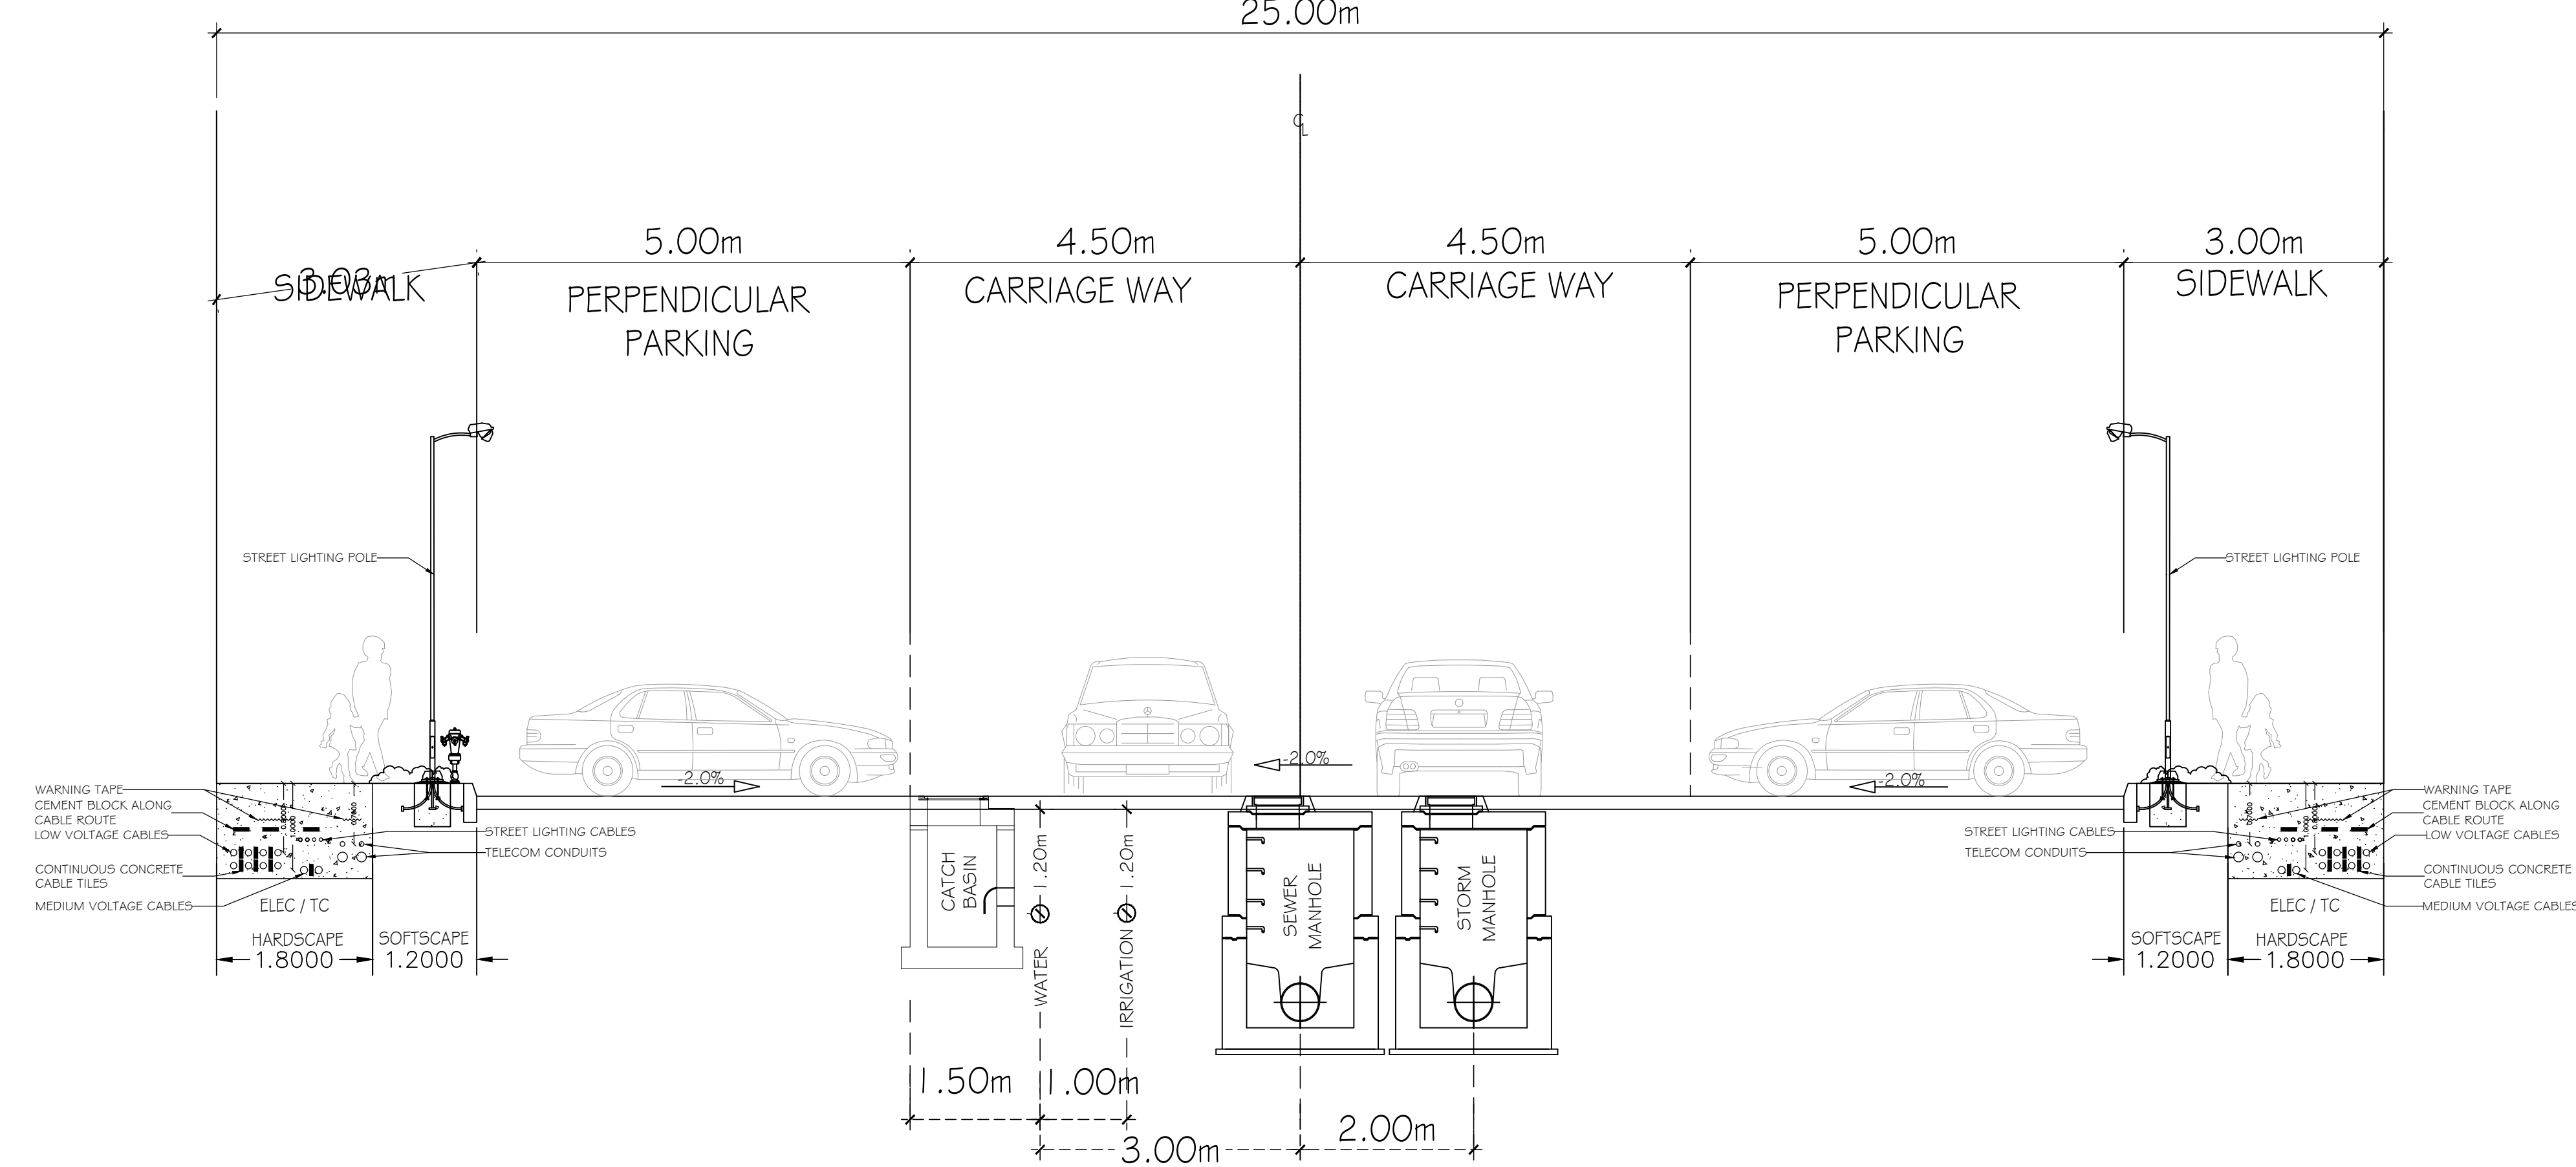

00	ISSUED FOR TENDER	JAN.2026
REV	DESCRIPTION	DATE
CLIENT:		
 MOUNTAIN VIEW a place to look up to CITY STAGES - OWNER DEVELOPMENT BY STAR CAPITAL AL PROJECT NUMBER: MOUNTAIN VIEW - PHASE 01 TEL: +966 440 111 1 - FAX: +966 440 111 1 - MOB: +966 15 15 15 15		
PROJECT NAME:		
 PHASE 01		
CONSULTANTS:		
 DESIGN ENGINEERING 87 El Mostahar Avenue, 2nd Floor, El Mostahar, El Mostahar, Cairo, Egypt. Tel: +966 2269 1566 / +966 2269 6309 / Web: www.dma.com.eg		
SHEET TITLE:		
UTILITY CROSS SECTION		
PART (1/3)		
SHEET REFERENCE NO:		
AL-C-SW-500	CHK	ZME
	RSS	APPR
	SCALE	NTS
PROJECT NO:		DMA/11/040-000
SHEET SERIAL NO:		01 OF 03
REVISION NO:		00