

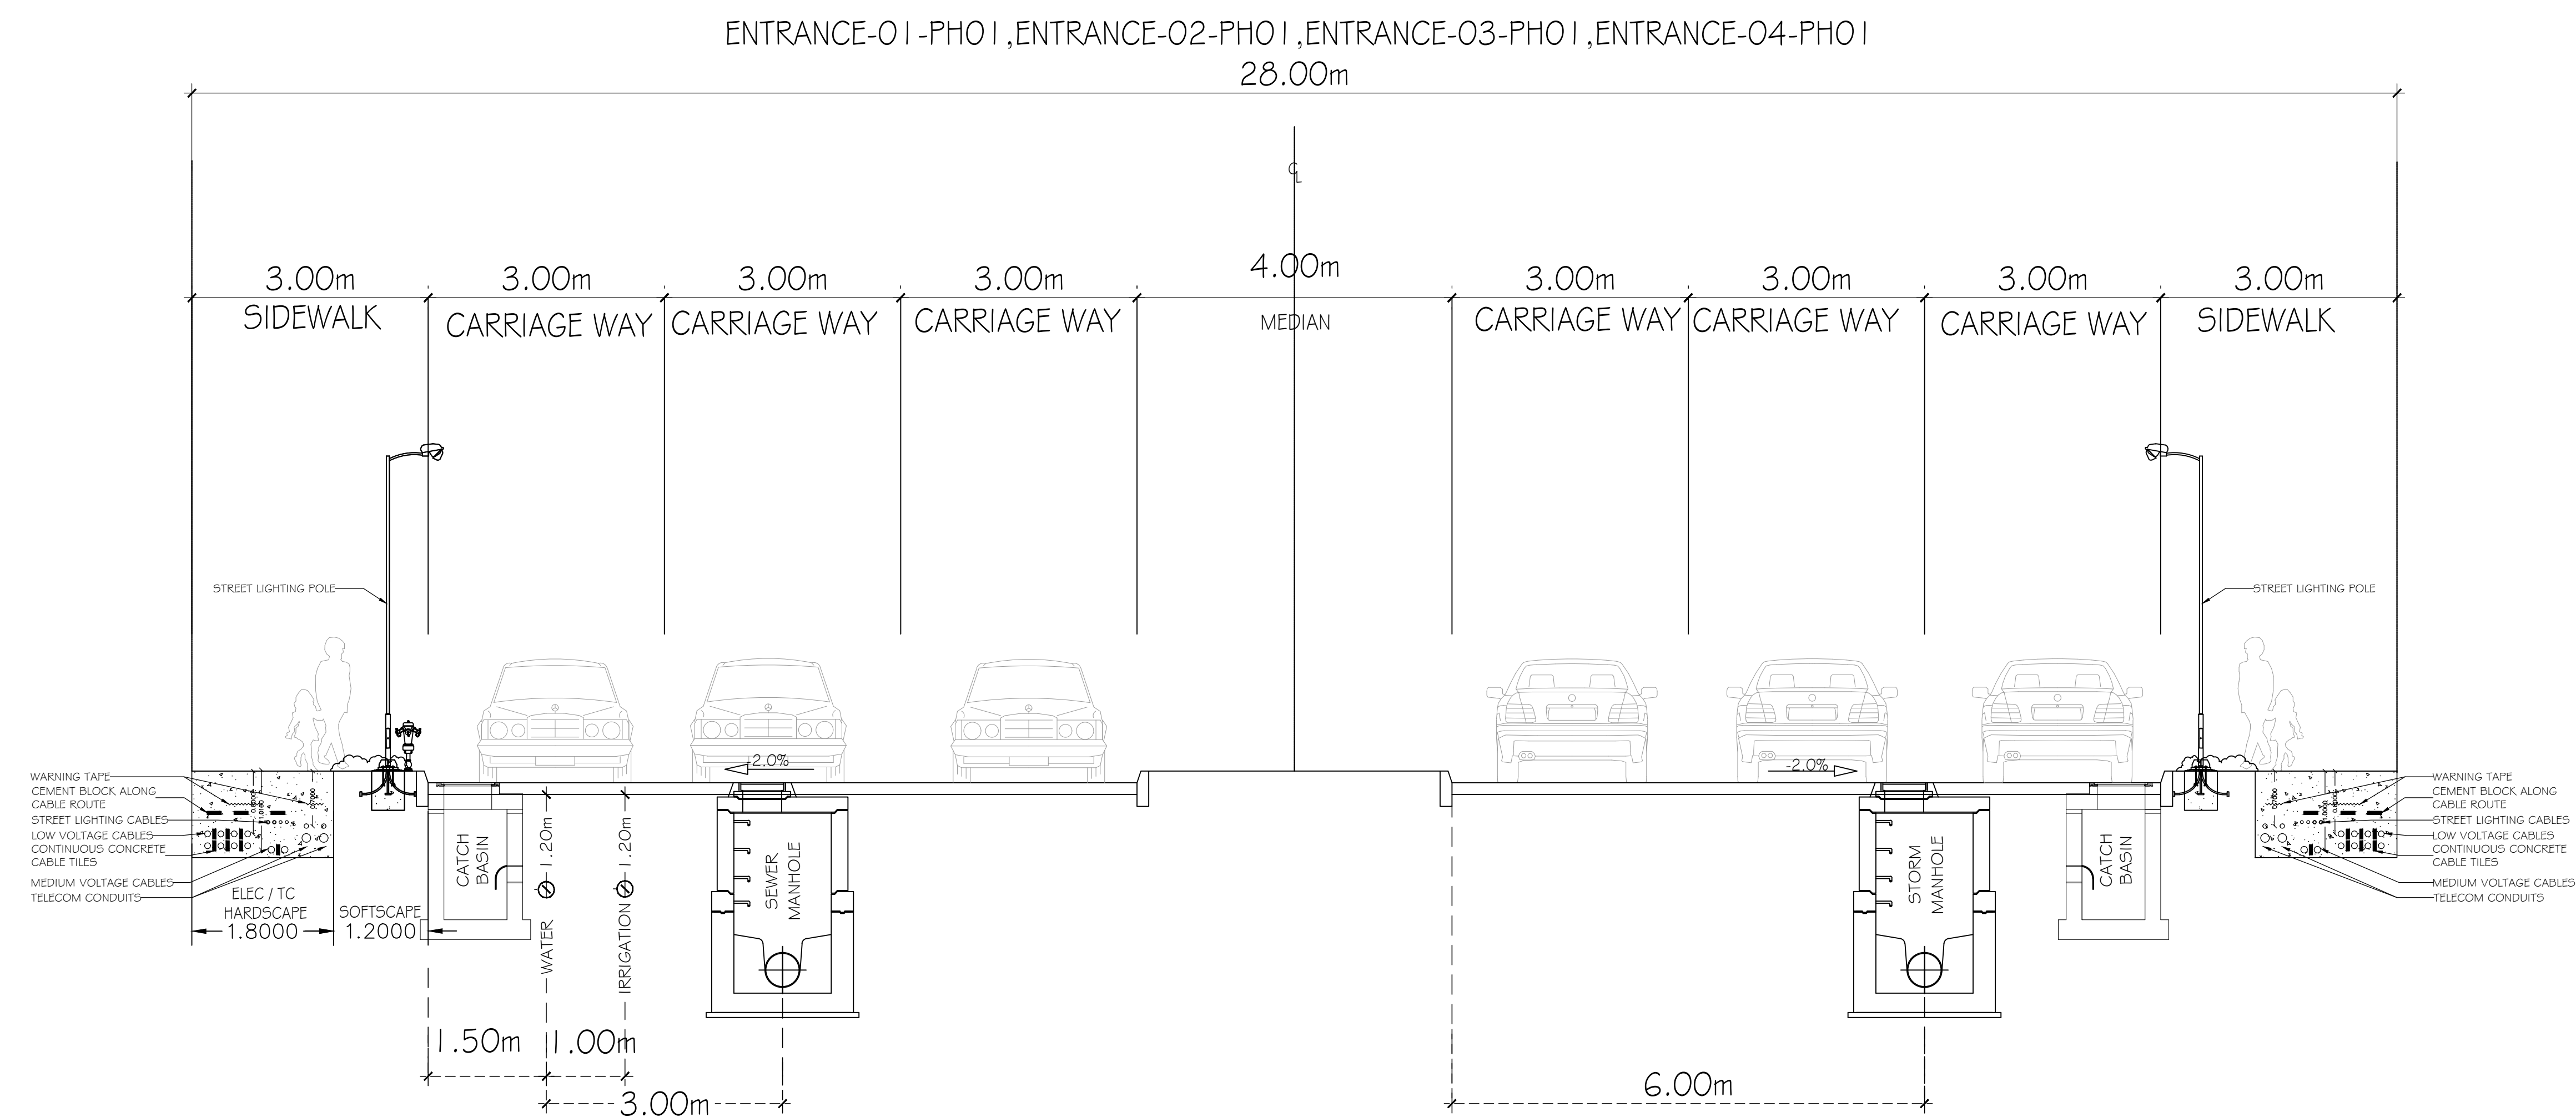


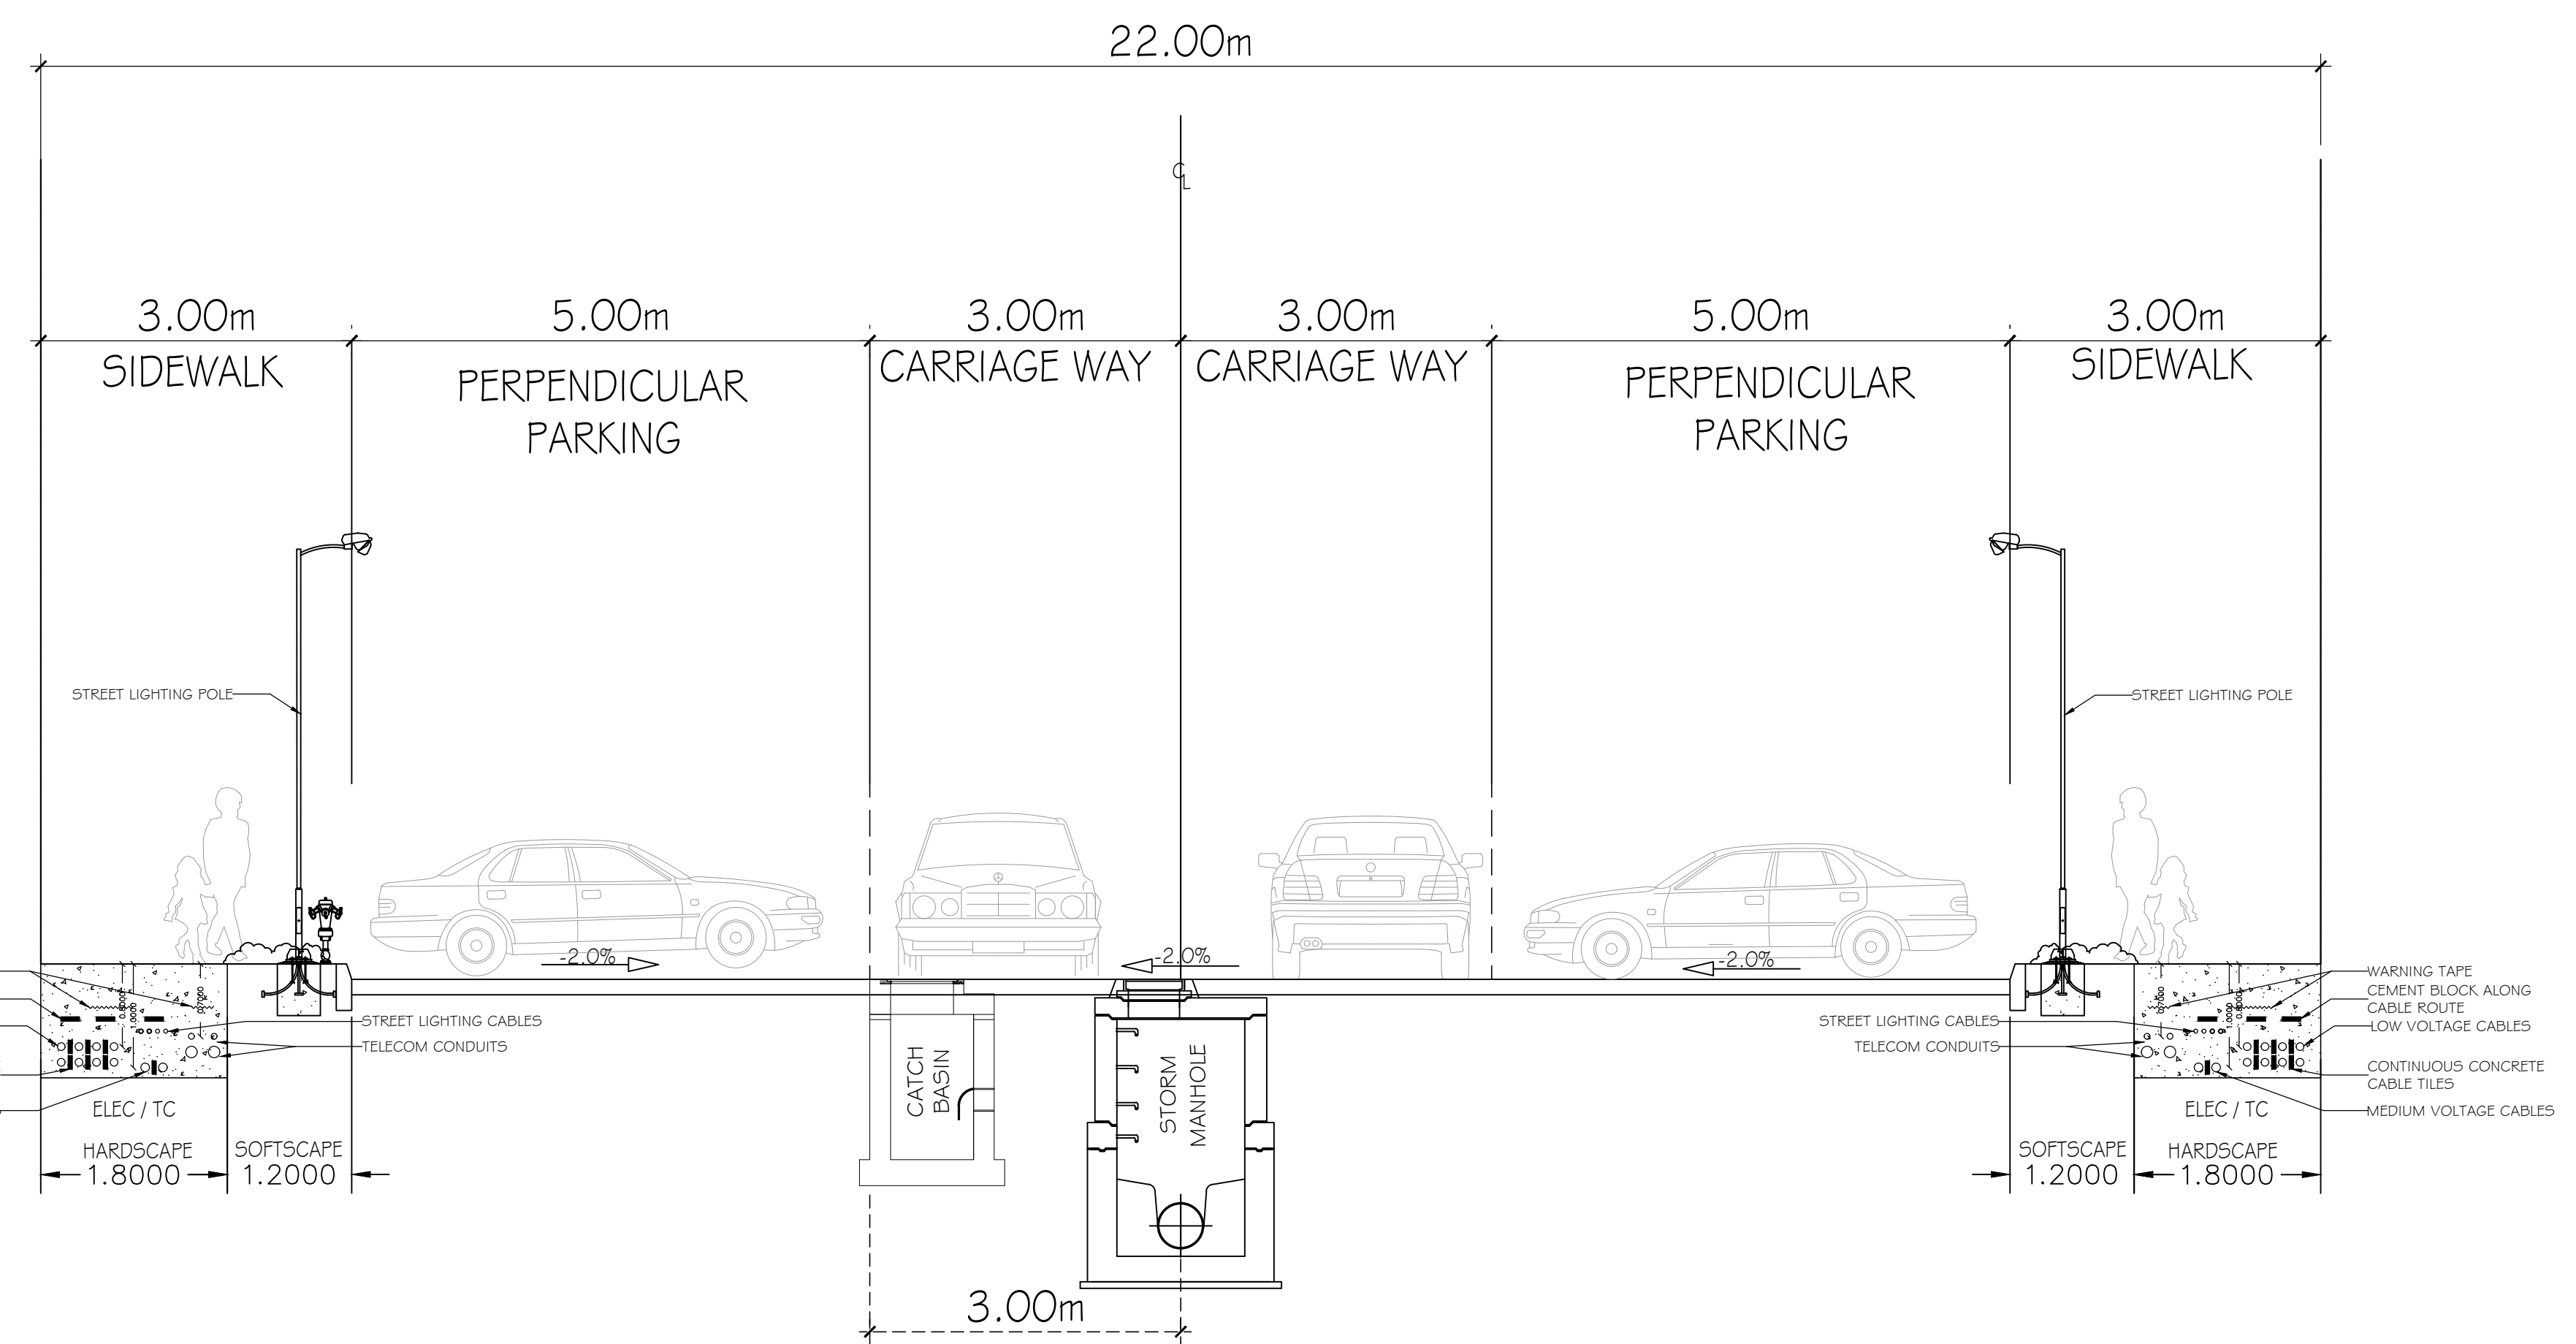

PARKING-01-PHOI, PARKING-07-PHOI, PARKING-09-PHOI, PARKING-11-PHOI, PARKING-13-PHOI, PARKING-16-PHOI, PARKING-17-PHOI, PARKING-18-PHOI
 PARKING-20-PHOI, PARKING-22-PHOI, PARKING-23-PHOI, PARKING-24-PHOI, PARKING-25-PHOI, PARKING-27-PHOI, PARKING-28-PHOI, PARKING-31-PHOI
 PARKING-32-PHOI, PARKING-33-PHOI, PARKING-34-PHOI, PARKING-35-PHOI, PARKING-38-PHOI, PARKING-39-PHOI, PARKING-40-PHOI, PARKING-41-PHOI
 PARKING-42-PHOI, PARKING-43-PHOI, PARKING-44-PHOI, PARKING-45-PHOI, PARKING-47-PHOI, PARKING-48-PHOI, PARKING-52-PHOI, PARKING-53-PHOI
 PARKING-54-PHOI, PARKING-55-PHOI

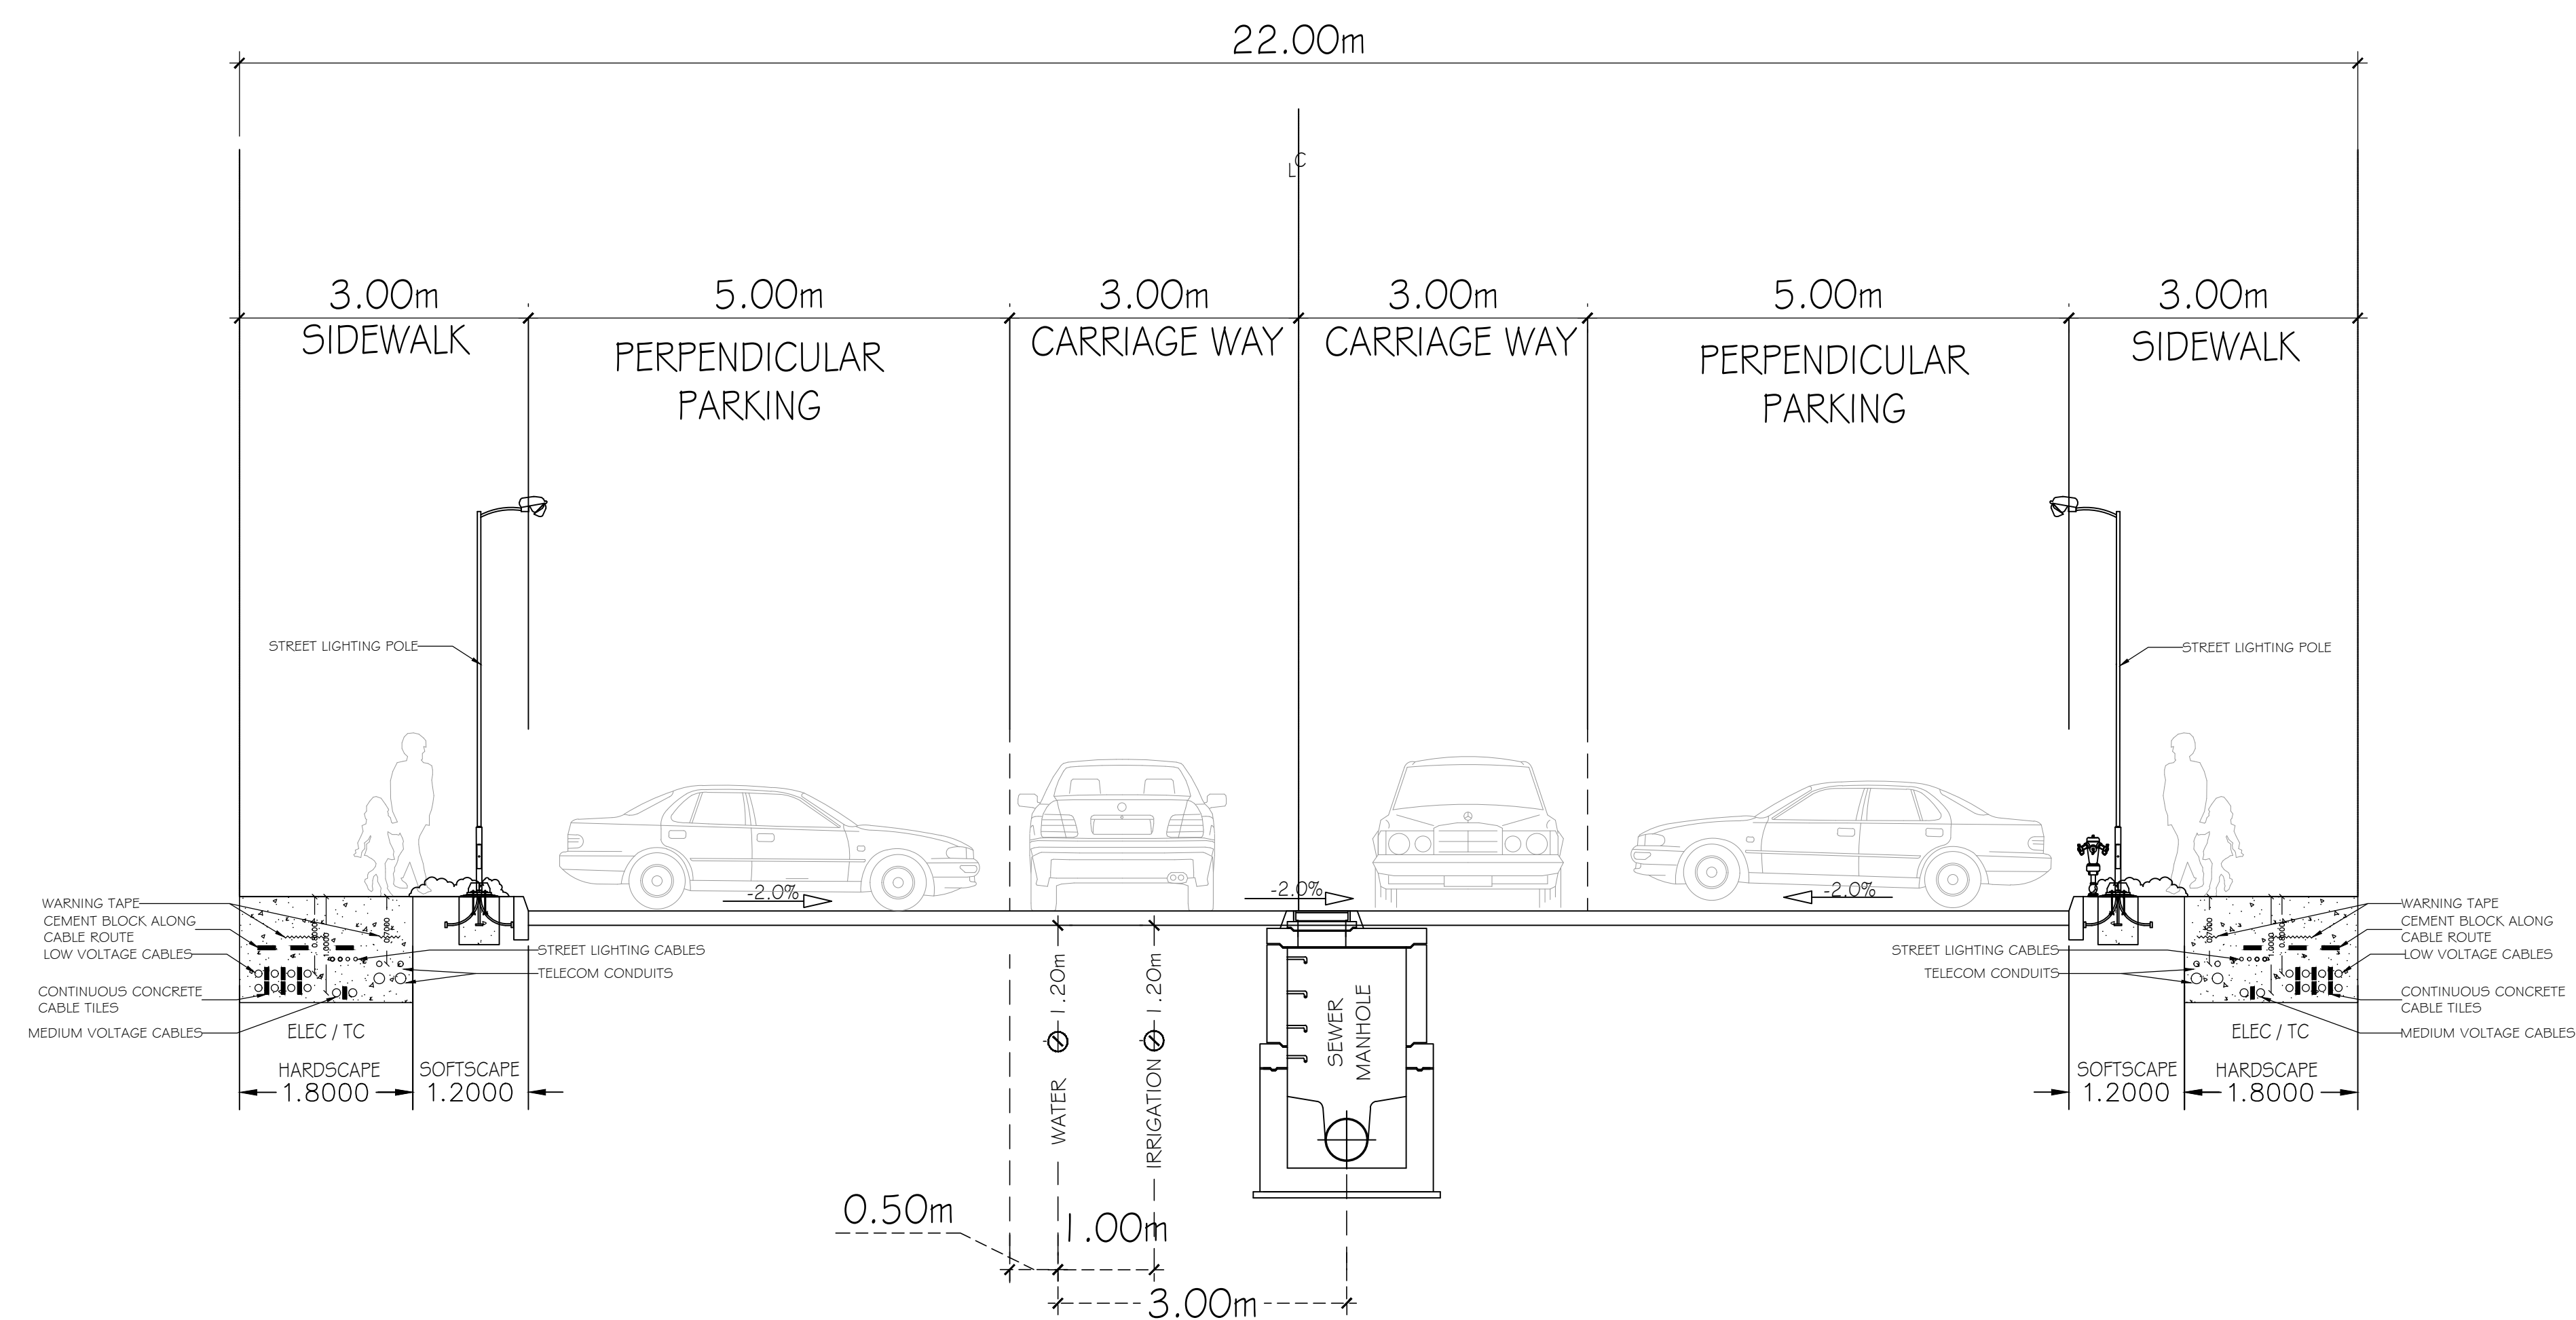

00	ISSUED FOR TENDER	JAN.2026
REV	DESCRIPTION	DATE
CLIENT:		
 CITY STAGES - OWNER DEVELOPER BY STADIUM CAPITAL PROJECT ADDRESS: 100, EL HELWAN, HELWAN GOV. TEL: +966 482 111 1 - FAX: +966 482 111 1 - MOB: +966 15 15 41		
PROJECT NAME:		
ALIVA PHASE 01		
CONSULTANTS:		
 87 El Mostahar Avenue, 2nd Floor, El Helwan, El Helwan, Cairo, Egypt Tel: +966 2269 7566 / +966 2269 6309 - Web: www.dma.com.eg		
SHEET TITLE:		
UTILITY CROSS SECTION PART (2/3)		
SHEET REFERENCE NO:	DRW	ZME
AL-C-SW-501	CHK	RSS
SCALE	NTS	APPR
PROJECT NO	DMA/11-040-000	HMS
SHEET SERIAL NO	02 OF 03	REVISION NO
		00