
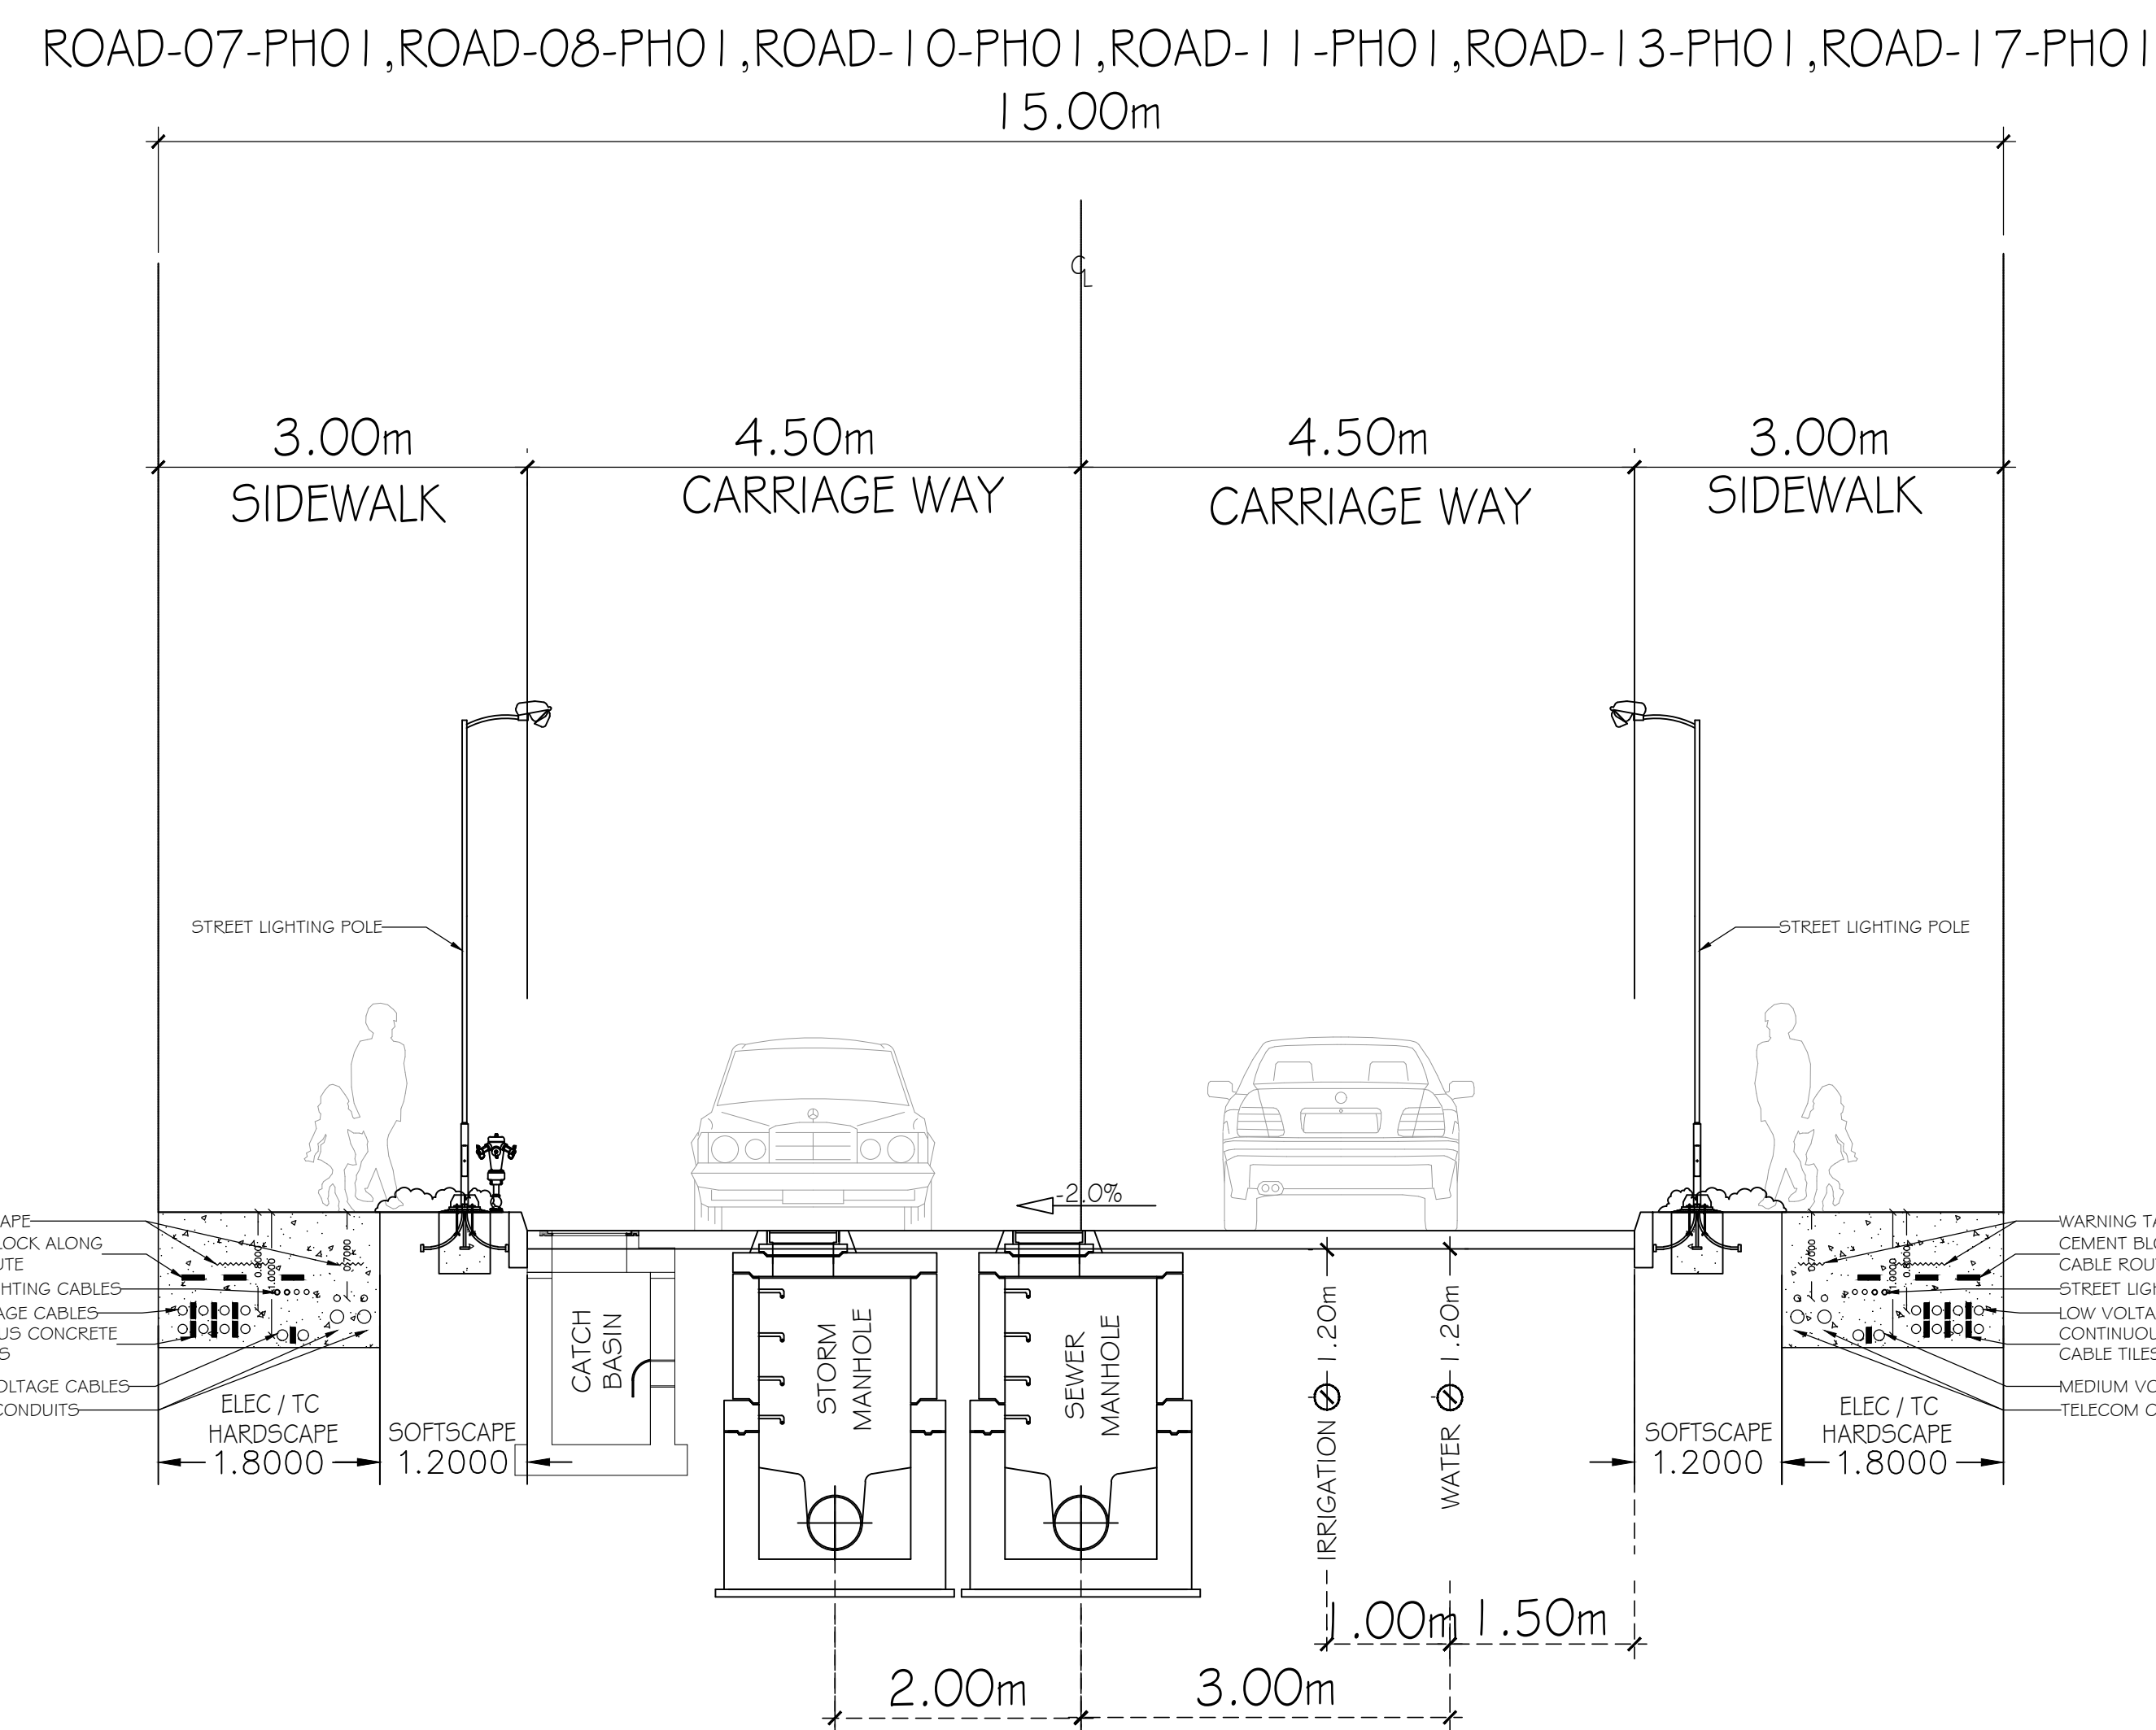
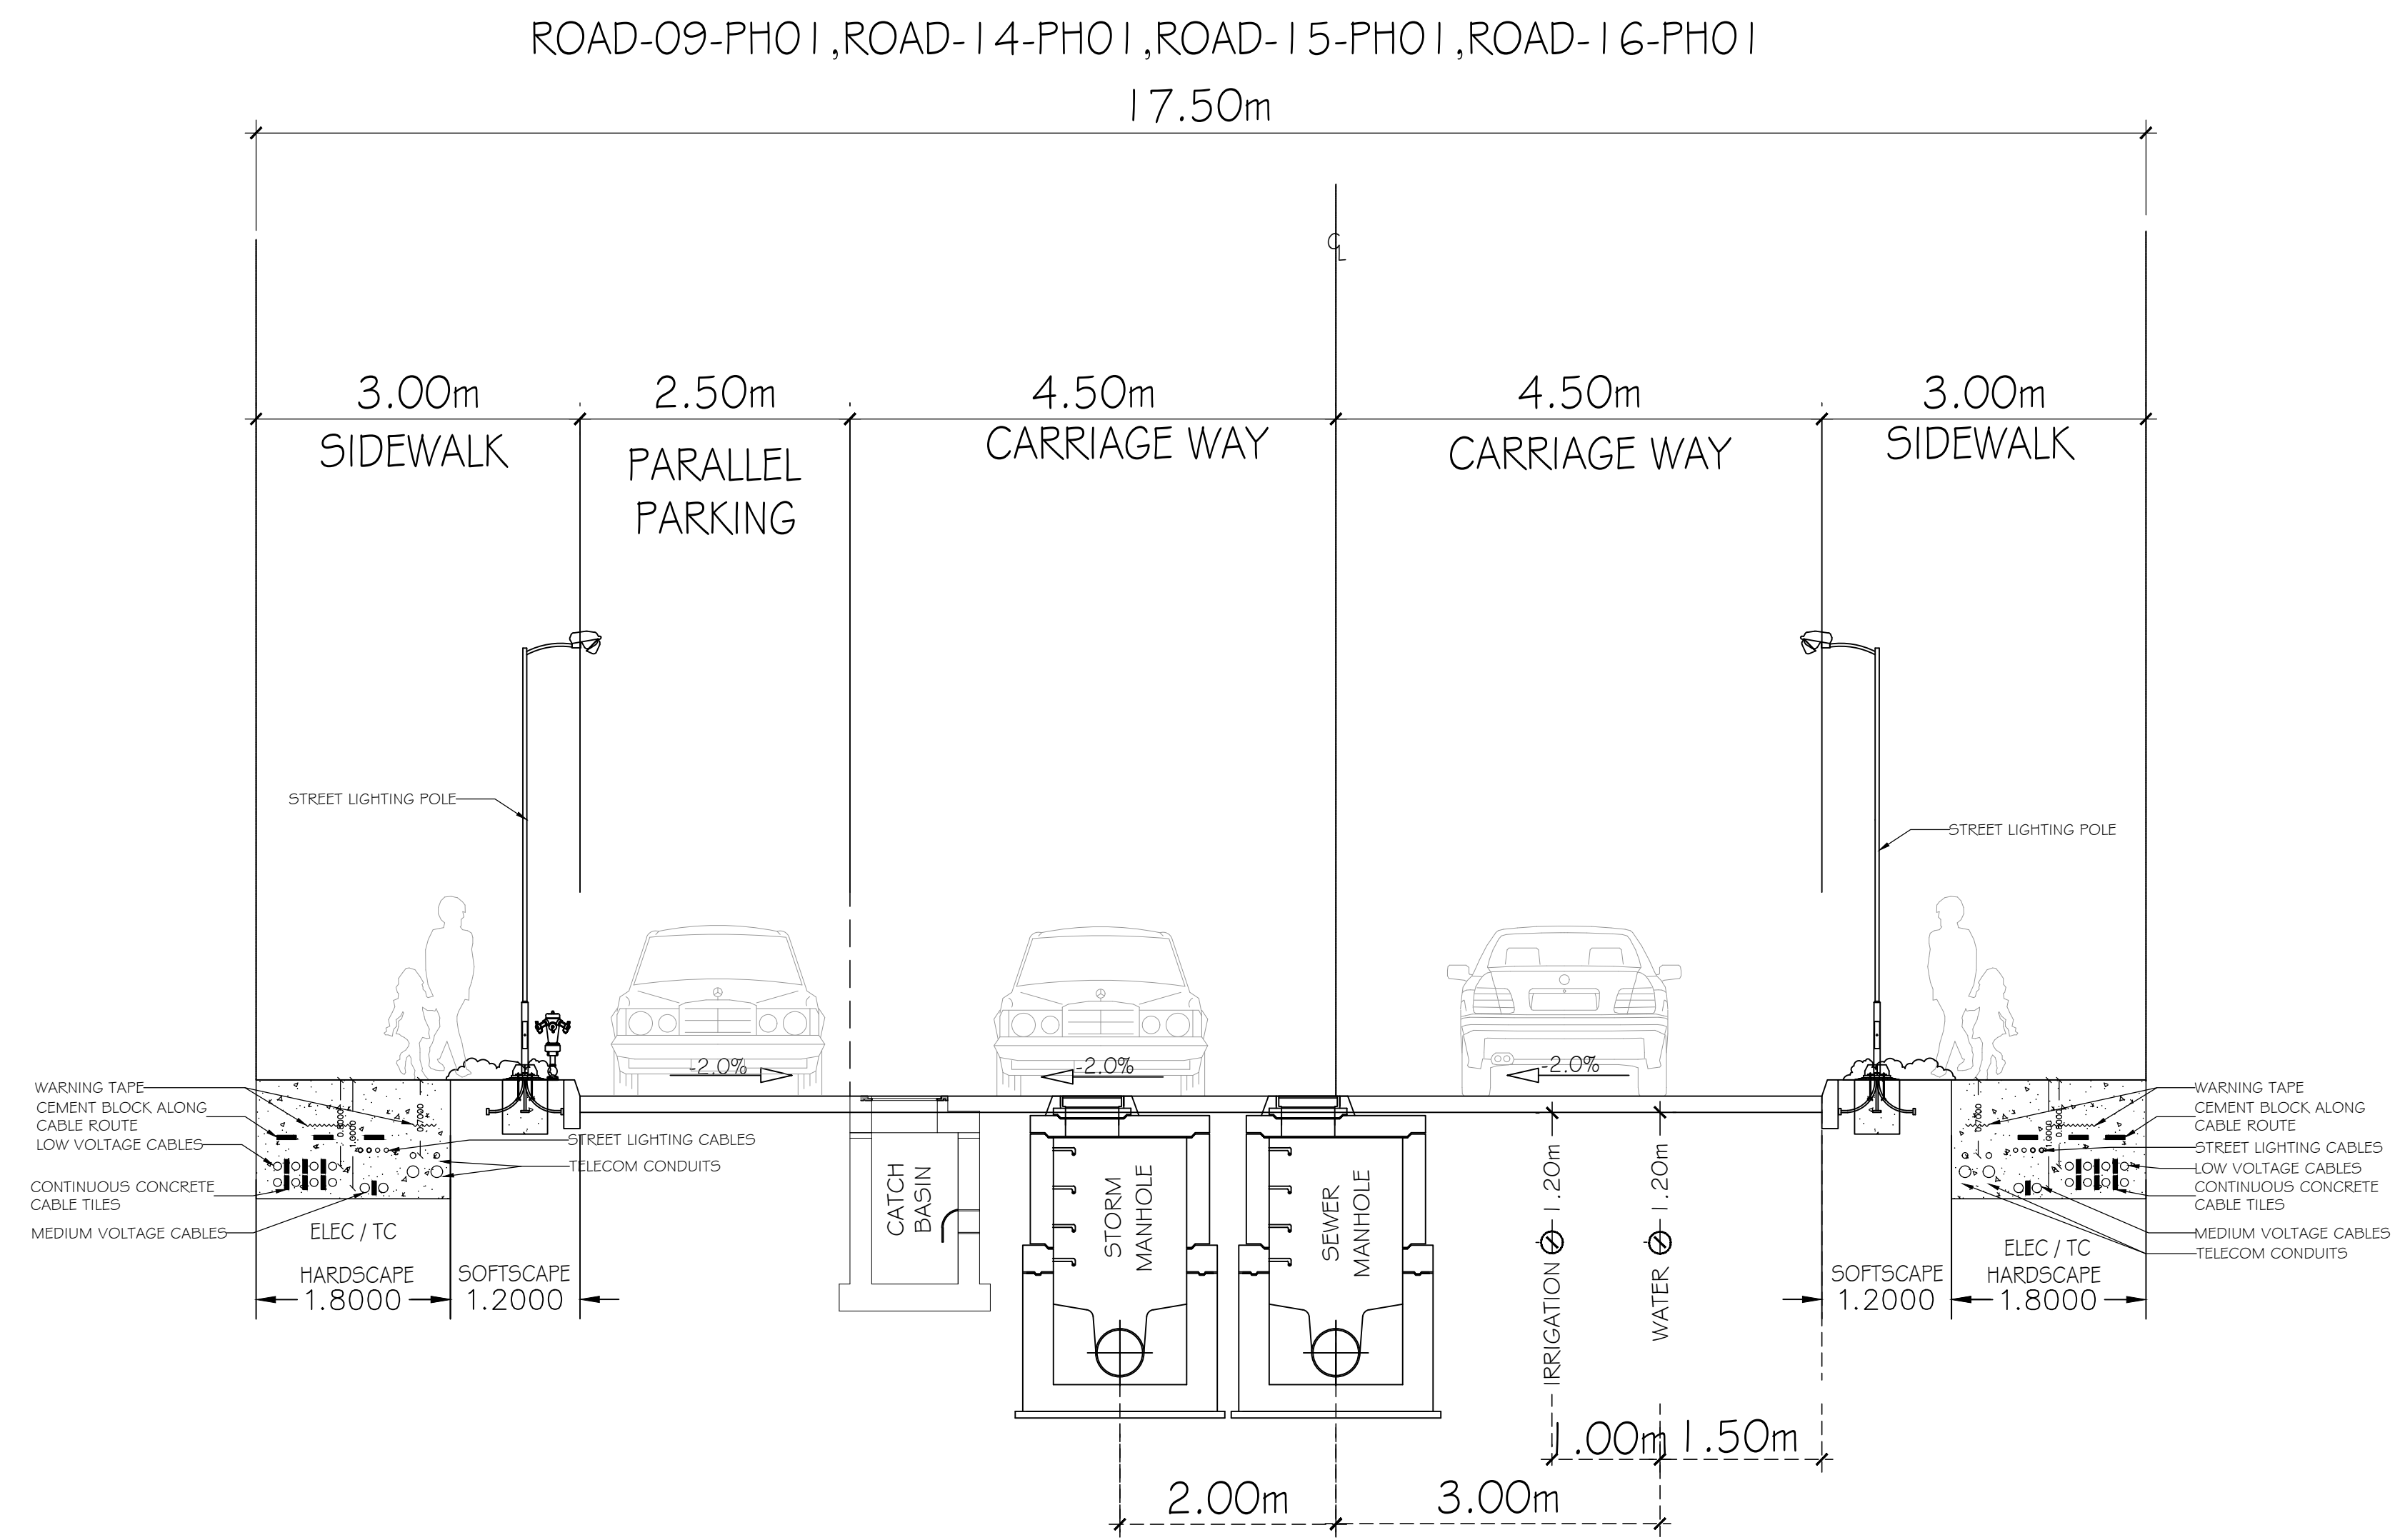


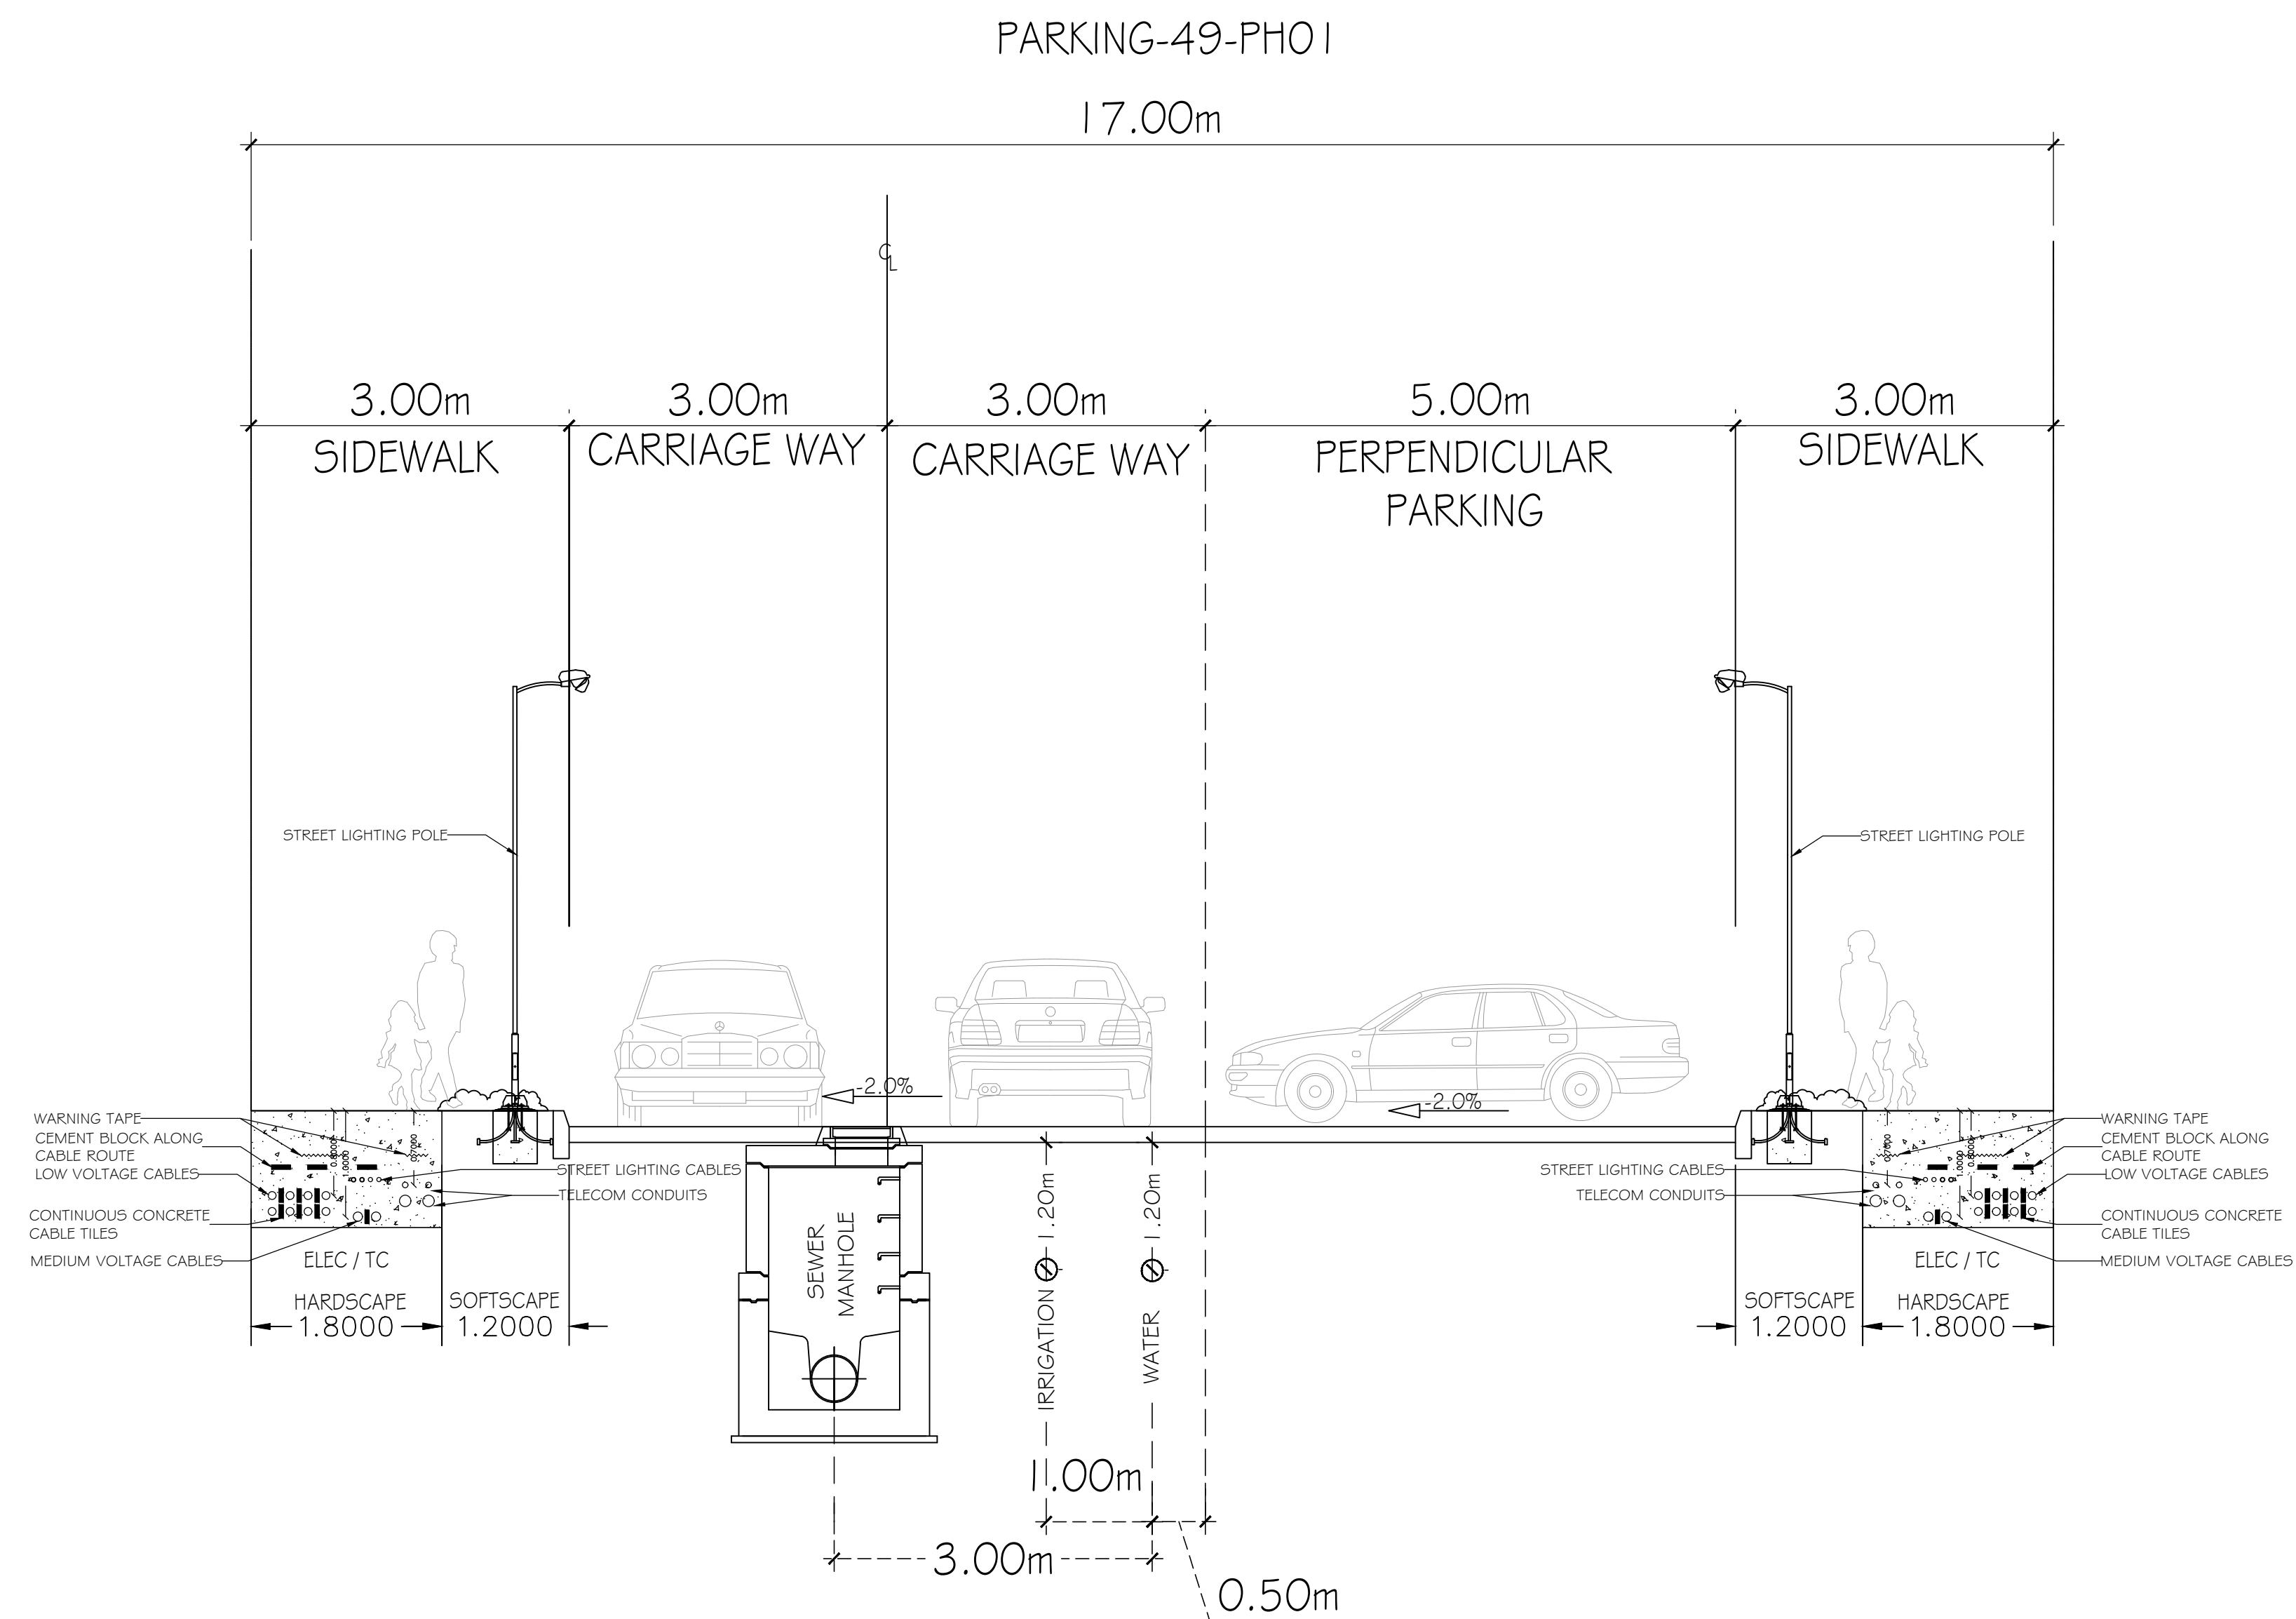

00	ISSUED FOR TENDER	JAN.2026	
REV	DESCRIPTION	DATE	
CLIENT:			
 MOUNTAIN VIEW a place to look up to CITY STAGES - OWNER DEVELOPER BY STAGE CAPITAL AL PROJECT NUMBER: MOUNTAIN VIEW STAGE CAPITAL AL TEL: +202 480 1111 - FAX: +202 480 1111 - MOB: +201015 11 41			
PROJECT NAME:			
ALIVA PHASE 01			
CONSULTANTS:			
 87 El Mostahar Avenue, 2nd Floor, El Mostahar, El Mostahar, Cairo, Egypt Tel: +202 2269 7566 / +202 2269 6309 - Web: www.dma.com.eg			
SHEET TITLE:			
UTILITY CROSS SECTION PART (3/3)			
SHEET REFERENCE NO:			
AL-C-SW-502			
DRW 2ME DSN 2ME CHK RSS APPRV HMS SCALE NTS			
PROJECT NO: DMA/11/040-000			
SHEET SERIAL NO: 03 OF 03			
REVISION NO: 00			