


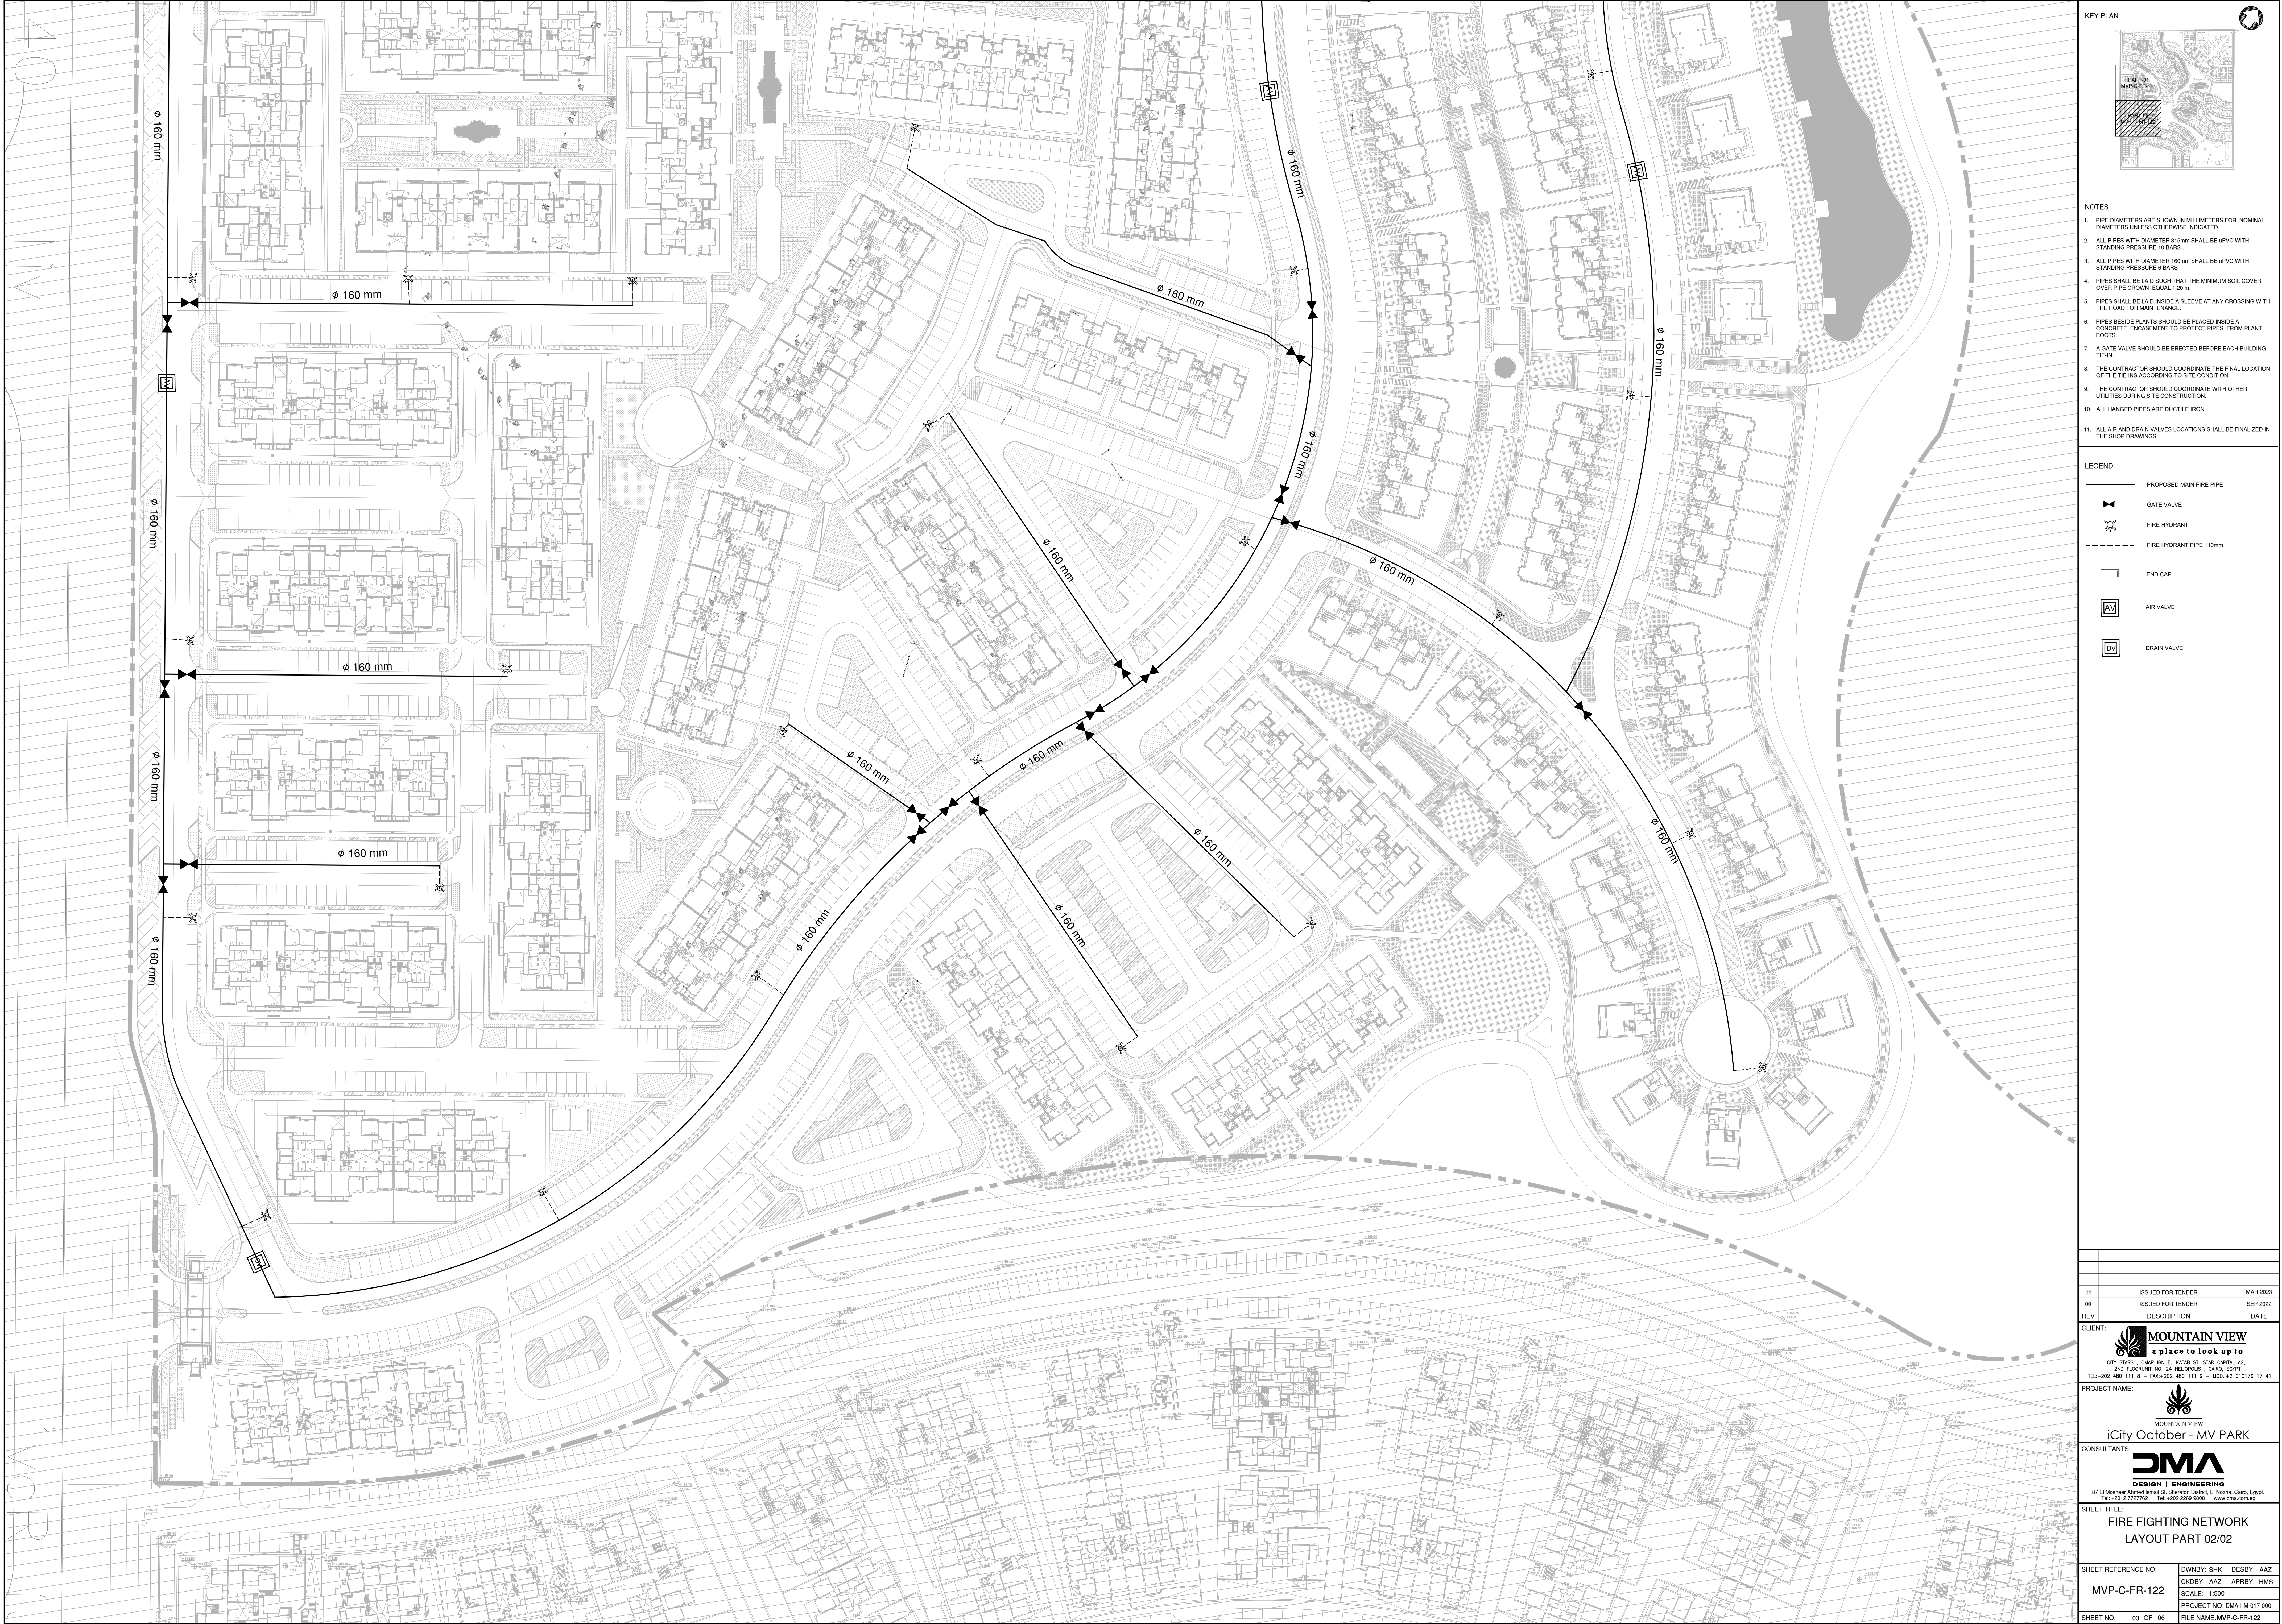

KEY PLAN

NOTES

1. PIPE DIAMETERS ARE SHOWN IN MILLIMETERS FOR NOMINAL DIAMETERS UNLESS OTHERWISE INDICATED.

2. ALL PIPES WITH DIAMETER 315mm SHALL BE UPVC WITH STANDING PRESSURE 10 BARS.

3. ALL PIPES WITH DIAMETER 160mm SHALL BE UPVC WITH STANDING PRESSURE 6 BARS.

4. PIPES SHALL BE LAID SUCH THAT THE MINIMUM SOIL COVER OVER PIPE CROWN EQUAL 1.20 m.

5. PIPES SHALL BE LAID INSIDE A SLEEVE AT ANY CROSSING WITH THE ROAD FOR MAINTENANCE.

6. PIPES BESIDE PLANTS SHOULD BE PLACED INSIDE A CONCRETE ENCASEMENT TO PROTECT PIPES FROM PLANT ROOTS.

7. A GATE VALVE SHOULD BE ERECTED BEFORE EACH BUILDING TIE-IN.

8. THE CONTRACTOR SHOULD COORDINATE THE FINAL LOCATION OF THE TIE INS ACCORDING TO SITE CONDITION.

9. THE CONTRACTOR SHOULD COORDINATE WITH OTHER UTILITIES DURING SITE CONSTRUCTION.

10. ALL HANGED PIPES ARE DUCTILE IRON.

11. ALL AIR AND DRAIN VALVES LOCATIONS SHALL BE FINALIZED IN THE SHOP DRAWINGS.

LEGEND

PROPOSED MAIN FIRE PIPE

GATE VALVE

FIRE HYDRANT

FIRE HYDRANT PIPE 110mm

END CAP

AIR VALVE

DRAIN VALVE

01	ISSUED FOR TENDER	MAR 2023
00	ISSUED FOR TENDER	SEP 2022
REV	DESCRIPTION	DATE

CLIENT:

MOUNTAIN VIEW

a place to look up to

CITY OFFICE - CAMP BAY EL KAYE ST. 53RD CENTRAL AZ
2ND FLOOR/RT NO. 24 HELIOPOLIS - CAIRO, EGYPT
TEL:+202 485 111 8 - FAX:+202 485 111 9 - MOB:+2 010176 17 41

PROJECT NAME:

MOUNTAIN VIEW

iCity October - MV PARK

CONSULTANTS:

DESIGN | ENGINEERING

87 El Motahar Ahmed Street St. Sheraton District, El Nadi, Cairo, Egypt
Tel: +202 7727755 Fax: +202 2989 8008 www.dma.com.eg

SHEET TITLE:

FIRE FIGHTING NETWORK

LAYOUT PART 02/02

SHEET REFERENCE NO:

DWBY: SHK DESBY: AAZ

CADBY: AAZ APPBY: HMS

MVP-C-FR-122

SCALE: 1:500

PROJECT NO: DMA-M-617-000

FILE NAME: MVP-C-FR-122

SHEET NO.

03 OF 06

PRINTED BY: ADAM ZAHER, PRINT DATE: Thursday, April 20, 2023, FILE PATH: H:\PROJECTS\ICITY OCT - MV PARK\06 CORRESPONDENCE\SET\SUBMITTALS\20230310 IFT - R01 02- FIRE FIGHTING NETWORK\CAD\WP-C-FR-122.DWG

COPYRIGHT NOTICE: THIS DRAWING AND ALL INFORMATION WITHIN ARE THE SOLE PROPERTY OF DMA CONSULTANTS. UNAUTHORIZED COPYING, REPRODUCTION, REDISTRIBUTION, OR USE OF THIS INFORMATION, IN WHOLE OR IN PART, WITHOUT WRITTEN CONSENT OF THE DMA CONSULTANTS, IS STRICTLY PROHIBITED. VIOLATIONS ARE LABEL FOR PROSECUTION UNDER THE EGYPTIAN AND INTERNATIONAL LAWS OF COPYRIGHT. © 2011 DMA CONSULTANTS ALL RIGHTS RESERVED